



ESTE PROJETO É DE PROPRIEDADE DA TRUCKVAN FICANDO PROIBIDA A SUA REPRODUÇÃO CONFORME PENALIDADES PREVISTA NAS LEIS.

REVISÃO	FOLHA	DESCRIÇÃO	ALT.	POR	DATA
A	2	LIBERADO	-	-	-

ESQUEMA ELÉTRICO DE POTÊNCIA

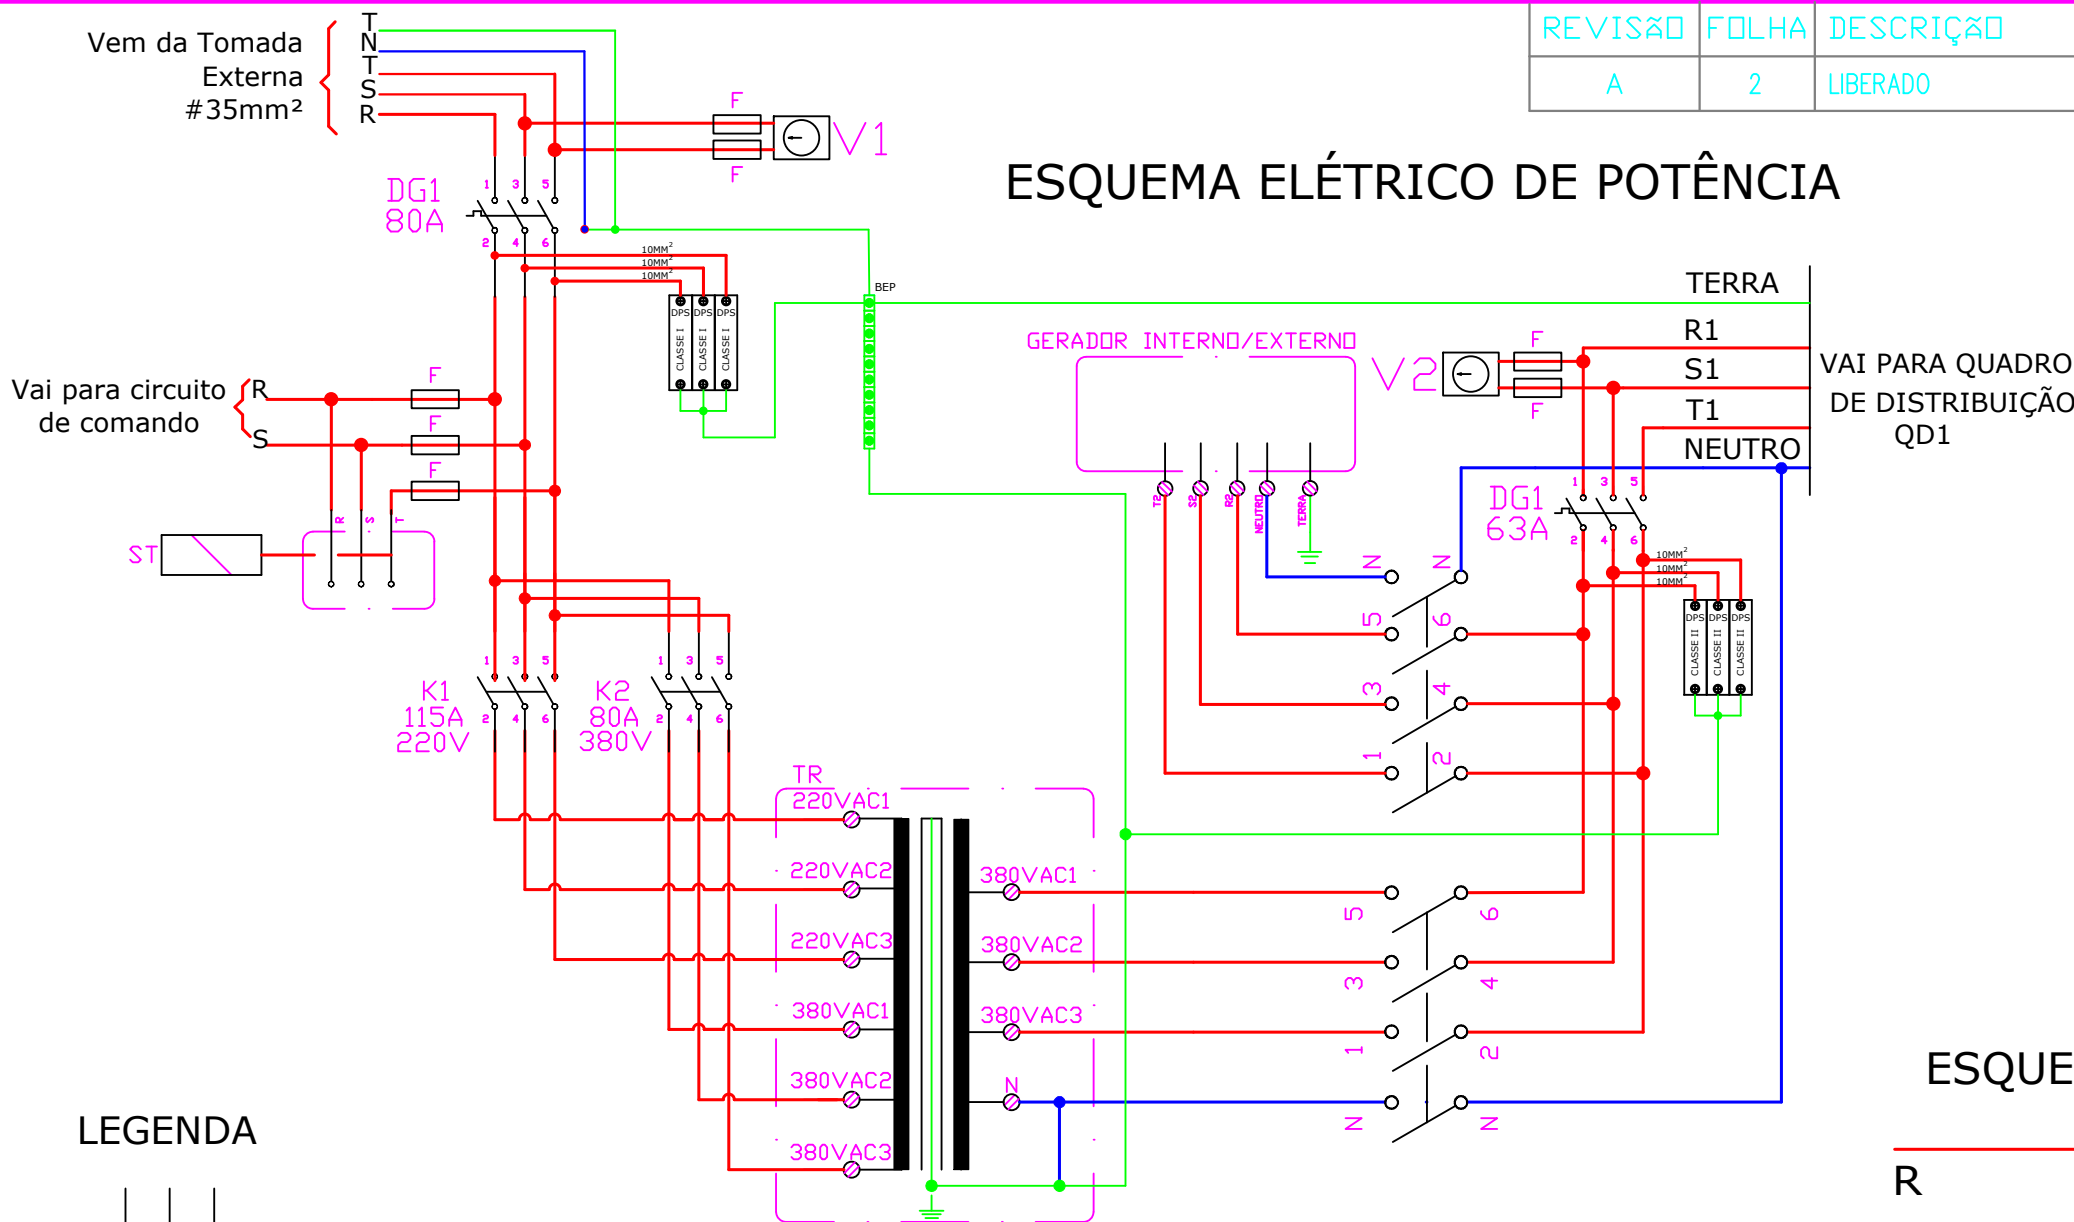

ESQUEMA ELÉTRICO DE COMANDO

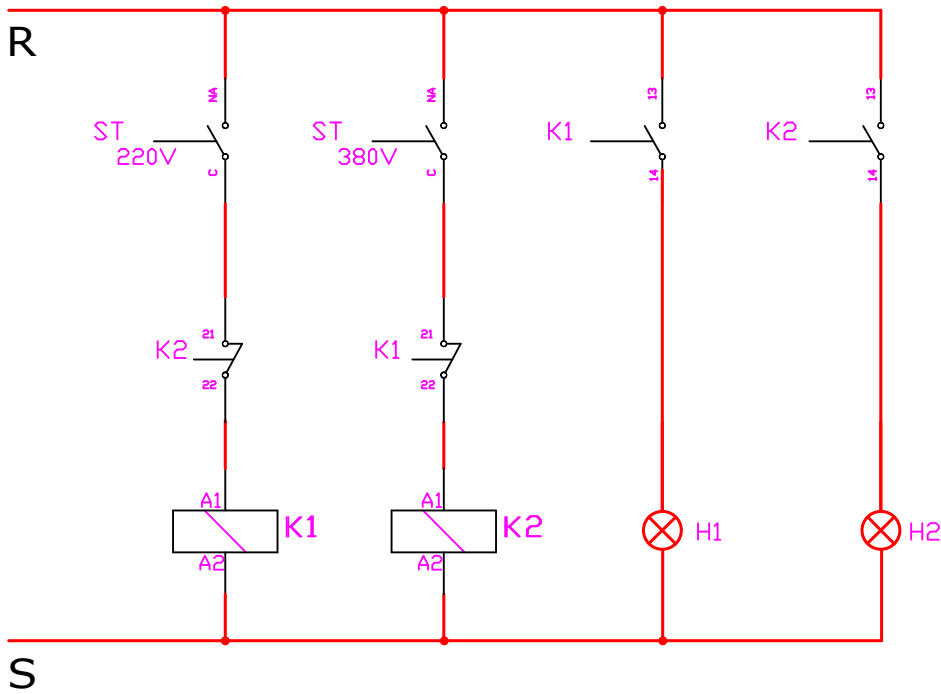

Instalações Elétricas conforme
Legislação e Norma ABNT 5410



CLASSE:	ELÉTRICA	PROJ/DES:	DOUGLAS	DATA:	29/07/26
GRUPO:	DIAGRAMA UNIFILAR	REVISADO:	MARCOS	DATA:	29/07/26
APLICAÇÃO:	SAÚDE	APROV.:	MARCOS	DATA:	29/07/26
TÍTULO:	DIAGRAMA DO QUADRO DE ENTRADA 1	ESC.:	S/E	UNID.:	-
CLIENTE:	BLUE HEALTH	CÓD.:		FORMATO:	A4
				FOLHA:	2 de 2