


ESTE PROJETO É DE PROPRIEDADE DA TRUCKVAN FICANDO PROIBIDA A SUA REPRODUÇÃO CONFORME PENALIDADES PREVISTA NAS LEIS.

REVISÃO	FOLHA	DESCRIÇÃO	ALT.	POR	DATA
A	2	LIBERADO	-	-	-

ESQUEMA ELÉTRICO DE POTÊNCIA

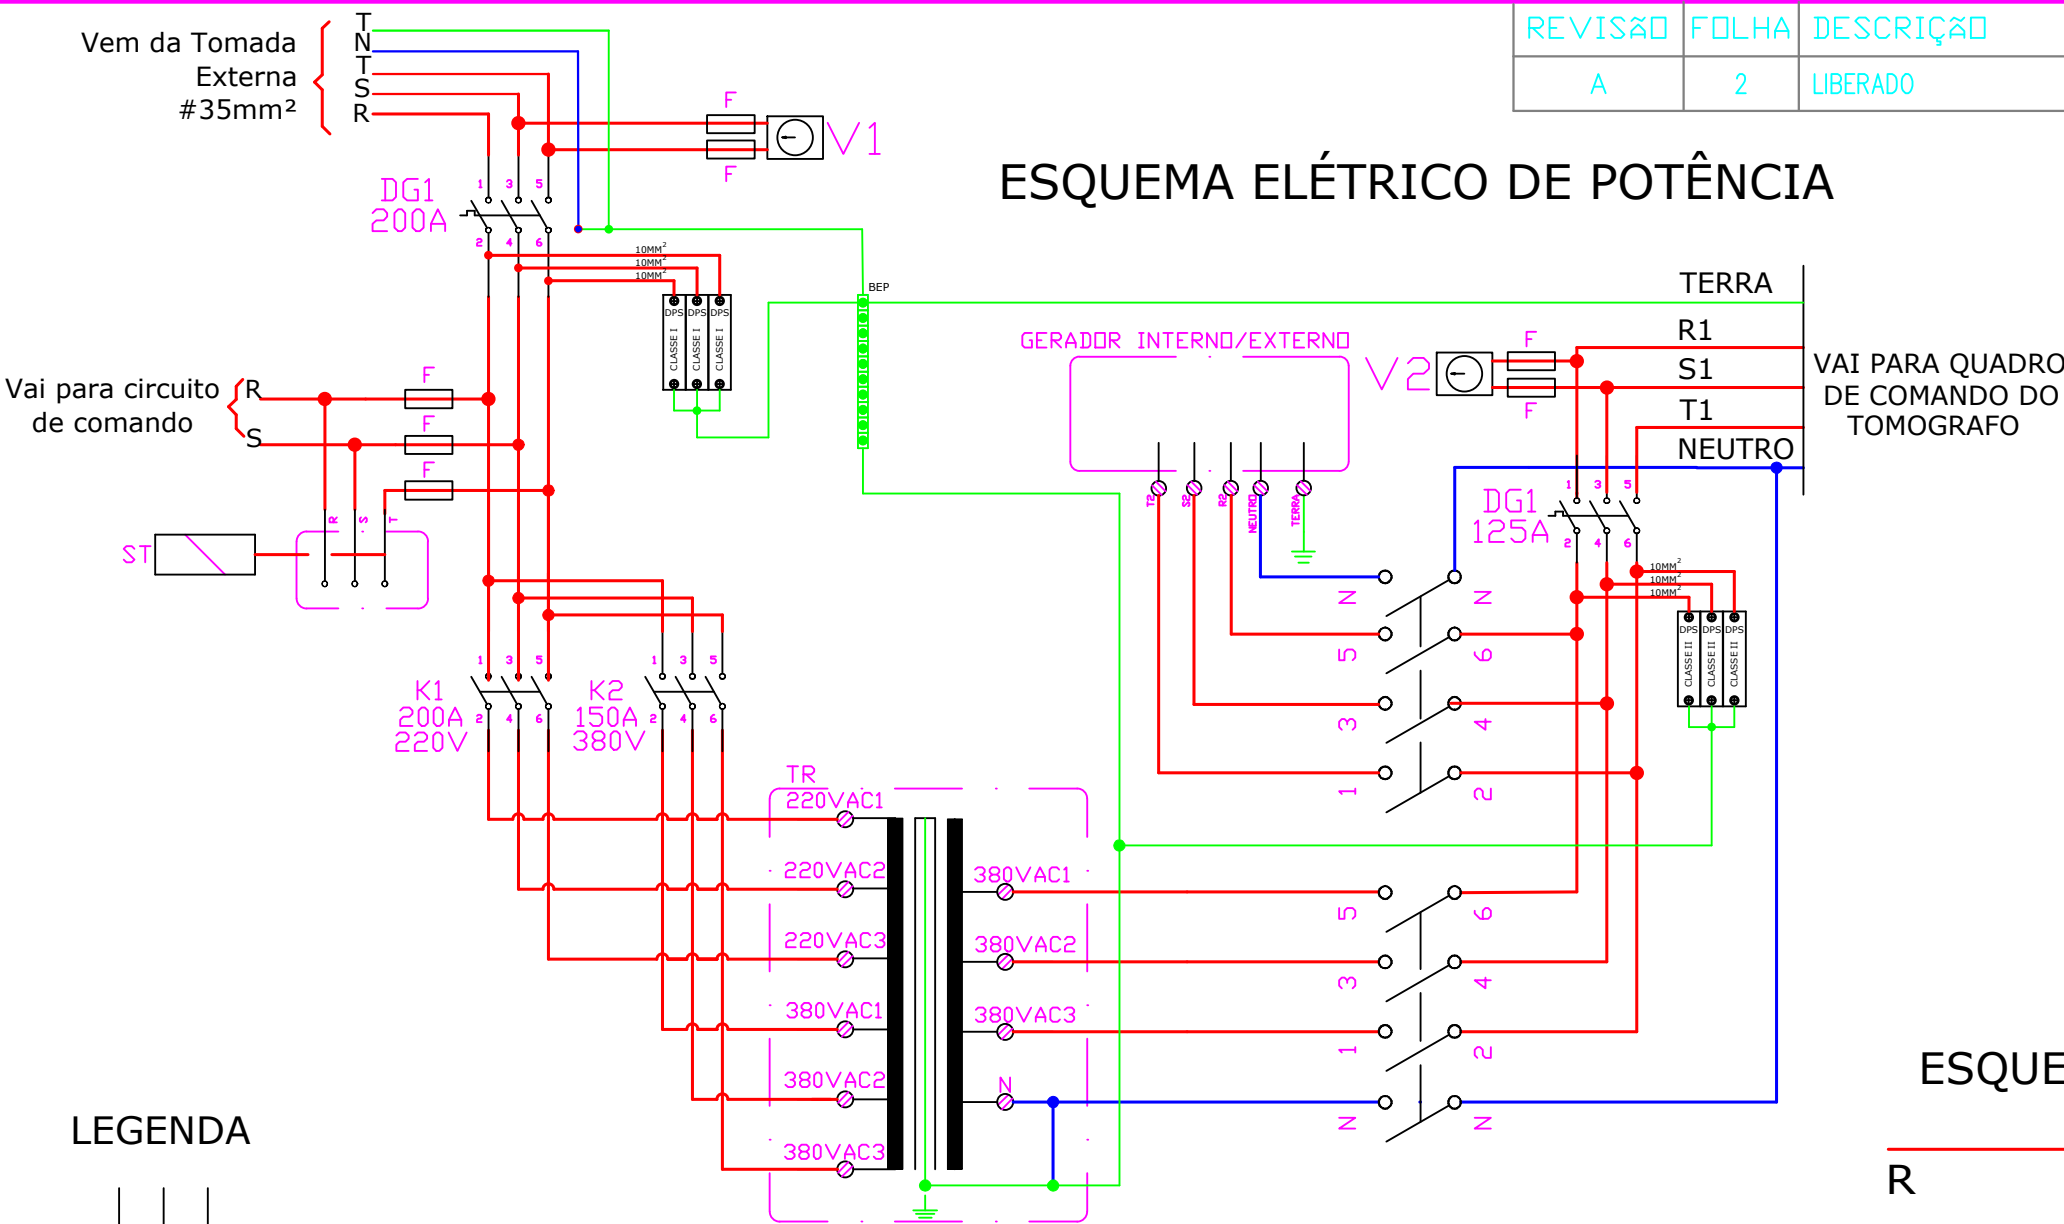

VAI PARA QUADRO DE COMANDO DO TOMOGRAFO

LEGENDA

Disjuntor Geral 200A

Potência: 70kVA
Primário: 220/380 V
Secundário: 380 V

Selecionador de Fase Automática

Contatos de Potência da Contatora.

Bobina da Contatora.

Contato Auxiliar NA do Selecionador de Fase


Contato Auxiliar NA da Contatora

FUSÍVEL

Indicação Visual

Voltímetro

ESQUEMA ELÉTRICO DE COMANDO

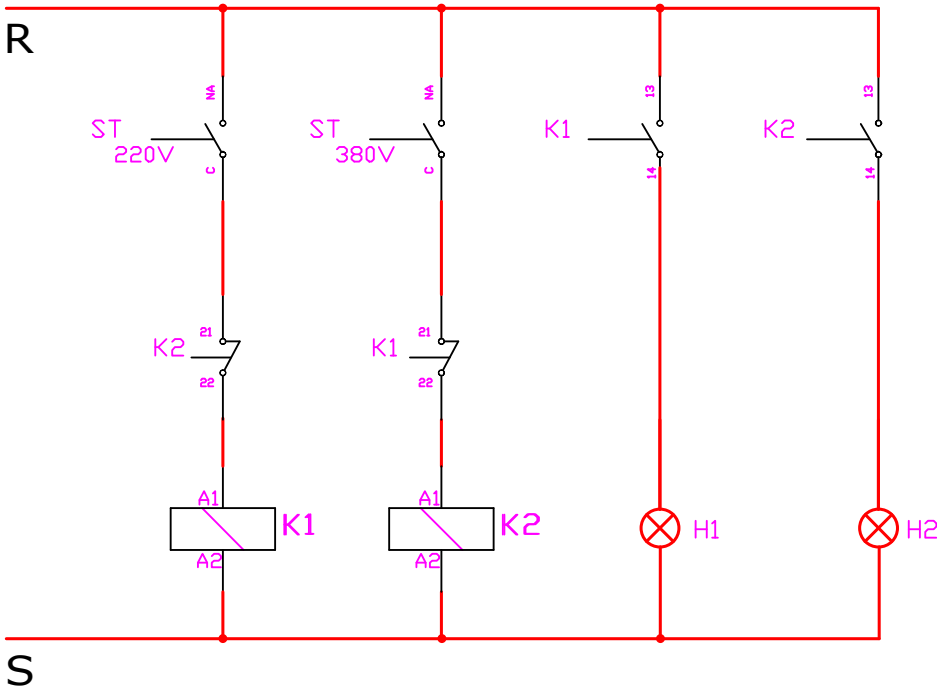

Instalações Elétricas conforme Legislação e Norma ABNT 5410	CLASSE:	ELÉTRICA	PROJ/DES:	DOUGLAS	DATA:	29/07/26
	GRUPO:	DIAGRAMA UNIFILAR	REVISADO:	MARCOS	DATA:	29/07/26
	APLICAÇÃO:	SAÚDE	APROV.:	MARCOS	DATA:	29/07/26
	TÍTULO:	DIAGRAMA DO QUADRO DE ENTRADA 2		ESC.:	S/E	UNID.: -
	CLIENTE:	BLUE HEALTH	CÓD.:		FORMATO:	A4
					FOLHA:	2 de 2