



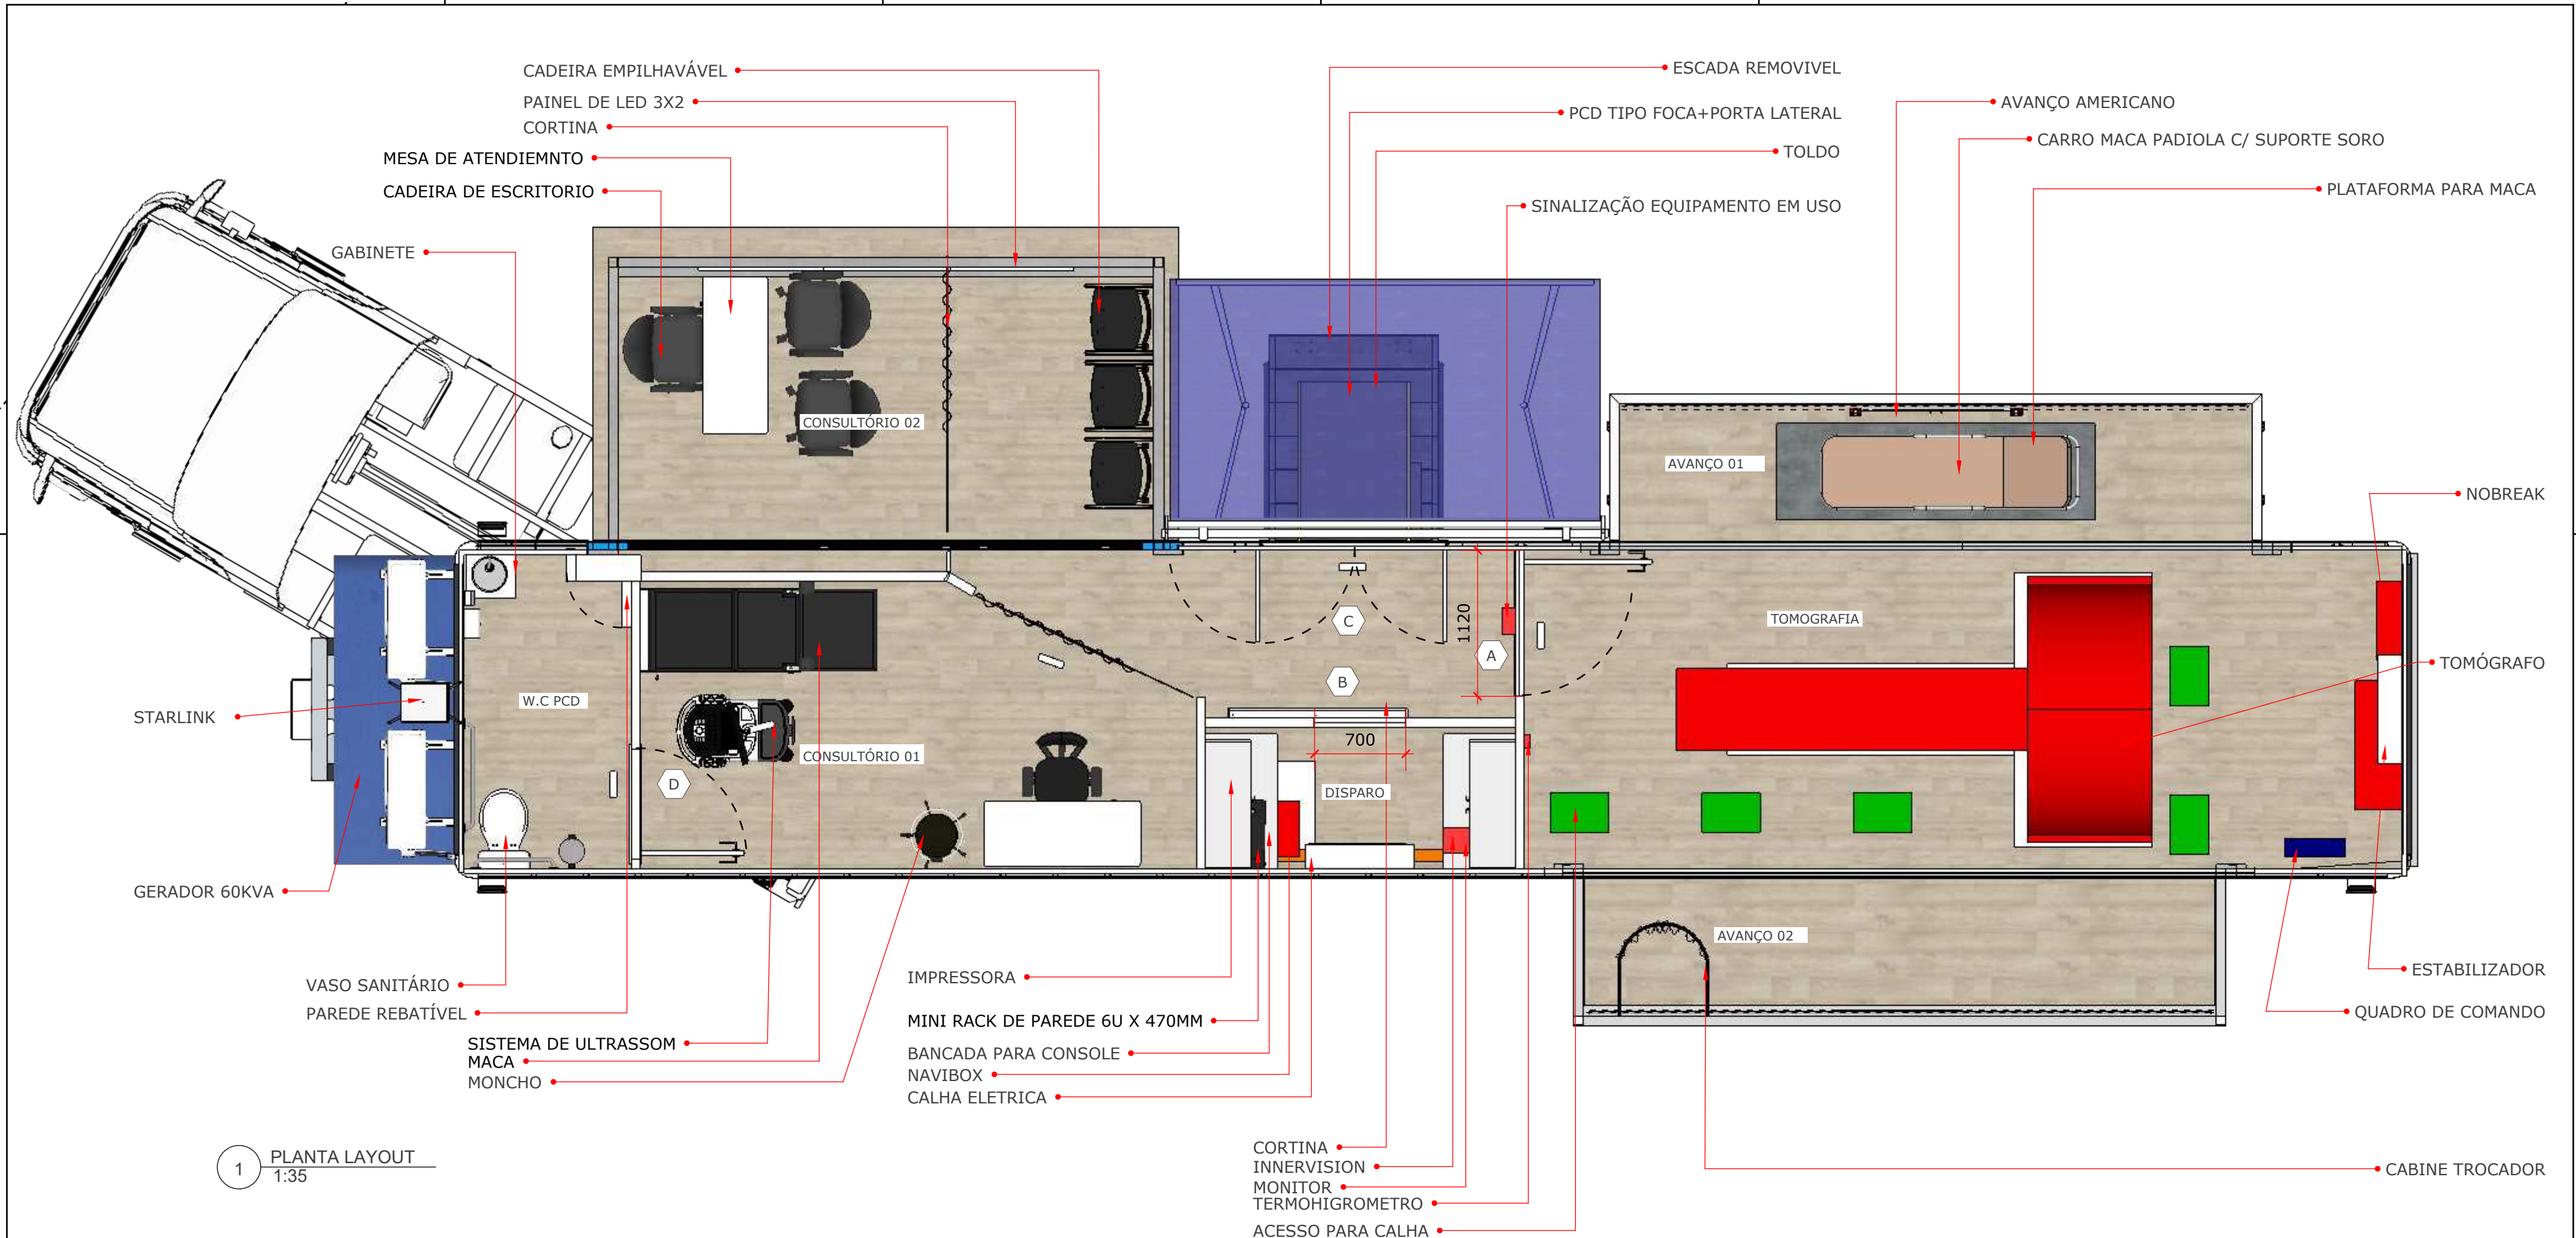

1 PLANTA LAYOUT
1:35

QUADRO DE PORTAS			
PORTA	TIPO	L VÃO	A VÃO
A	GIRO	1120	2100
B	CORRER	700	2100
C	BANG-BANG	1400	2100
D	GIRO	850	2000



MATERIAL	QTD	UNIDADE	ACABAMENTO	APLICAÇÃO
MDF	86	M²	BRANCO ALTO BRILHO KR 1330 ALUCO MAX	TETO
ACM	20	UN.	BRANCO ALTO BRILHO KR 1330 ALUCO MAX	PAREDE
COMPENSADO				
VINÍLICO	86	M²	PISO VINÍLICO TARKETT - CLIFF OAK NATURAL	PISO
FASE	REVISÃO	DATA	DESCRIÇÃO DA REVISÃO	
PE	R00	20/07/2026	INICIAL	
OBS:				
Pedido:	15741	Ref. Comercial:	0.0.2026.1.7.4.AA	1
Projeto:	360	Cliente:	BLUE HEALTH	
Arquivo:	PE-15741-R00	Aplicação:	LAYOUT	17
		Escala:	1:40	
		Projetista:	Karla Souza	
		Aprovação:	Victor Dariano	
		Data:	20 / 07 / 2026	

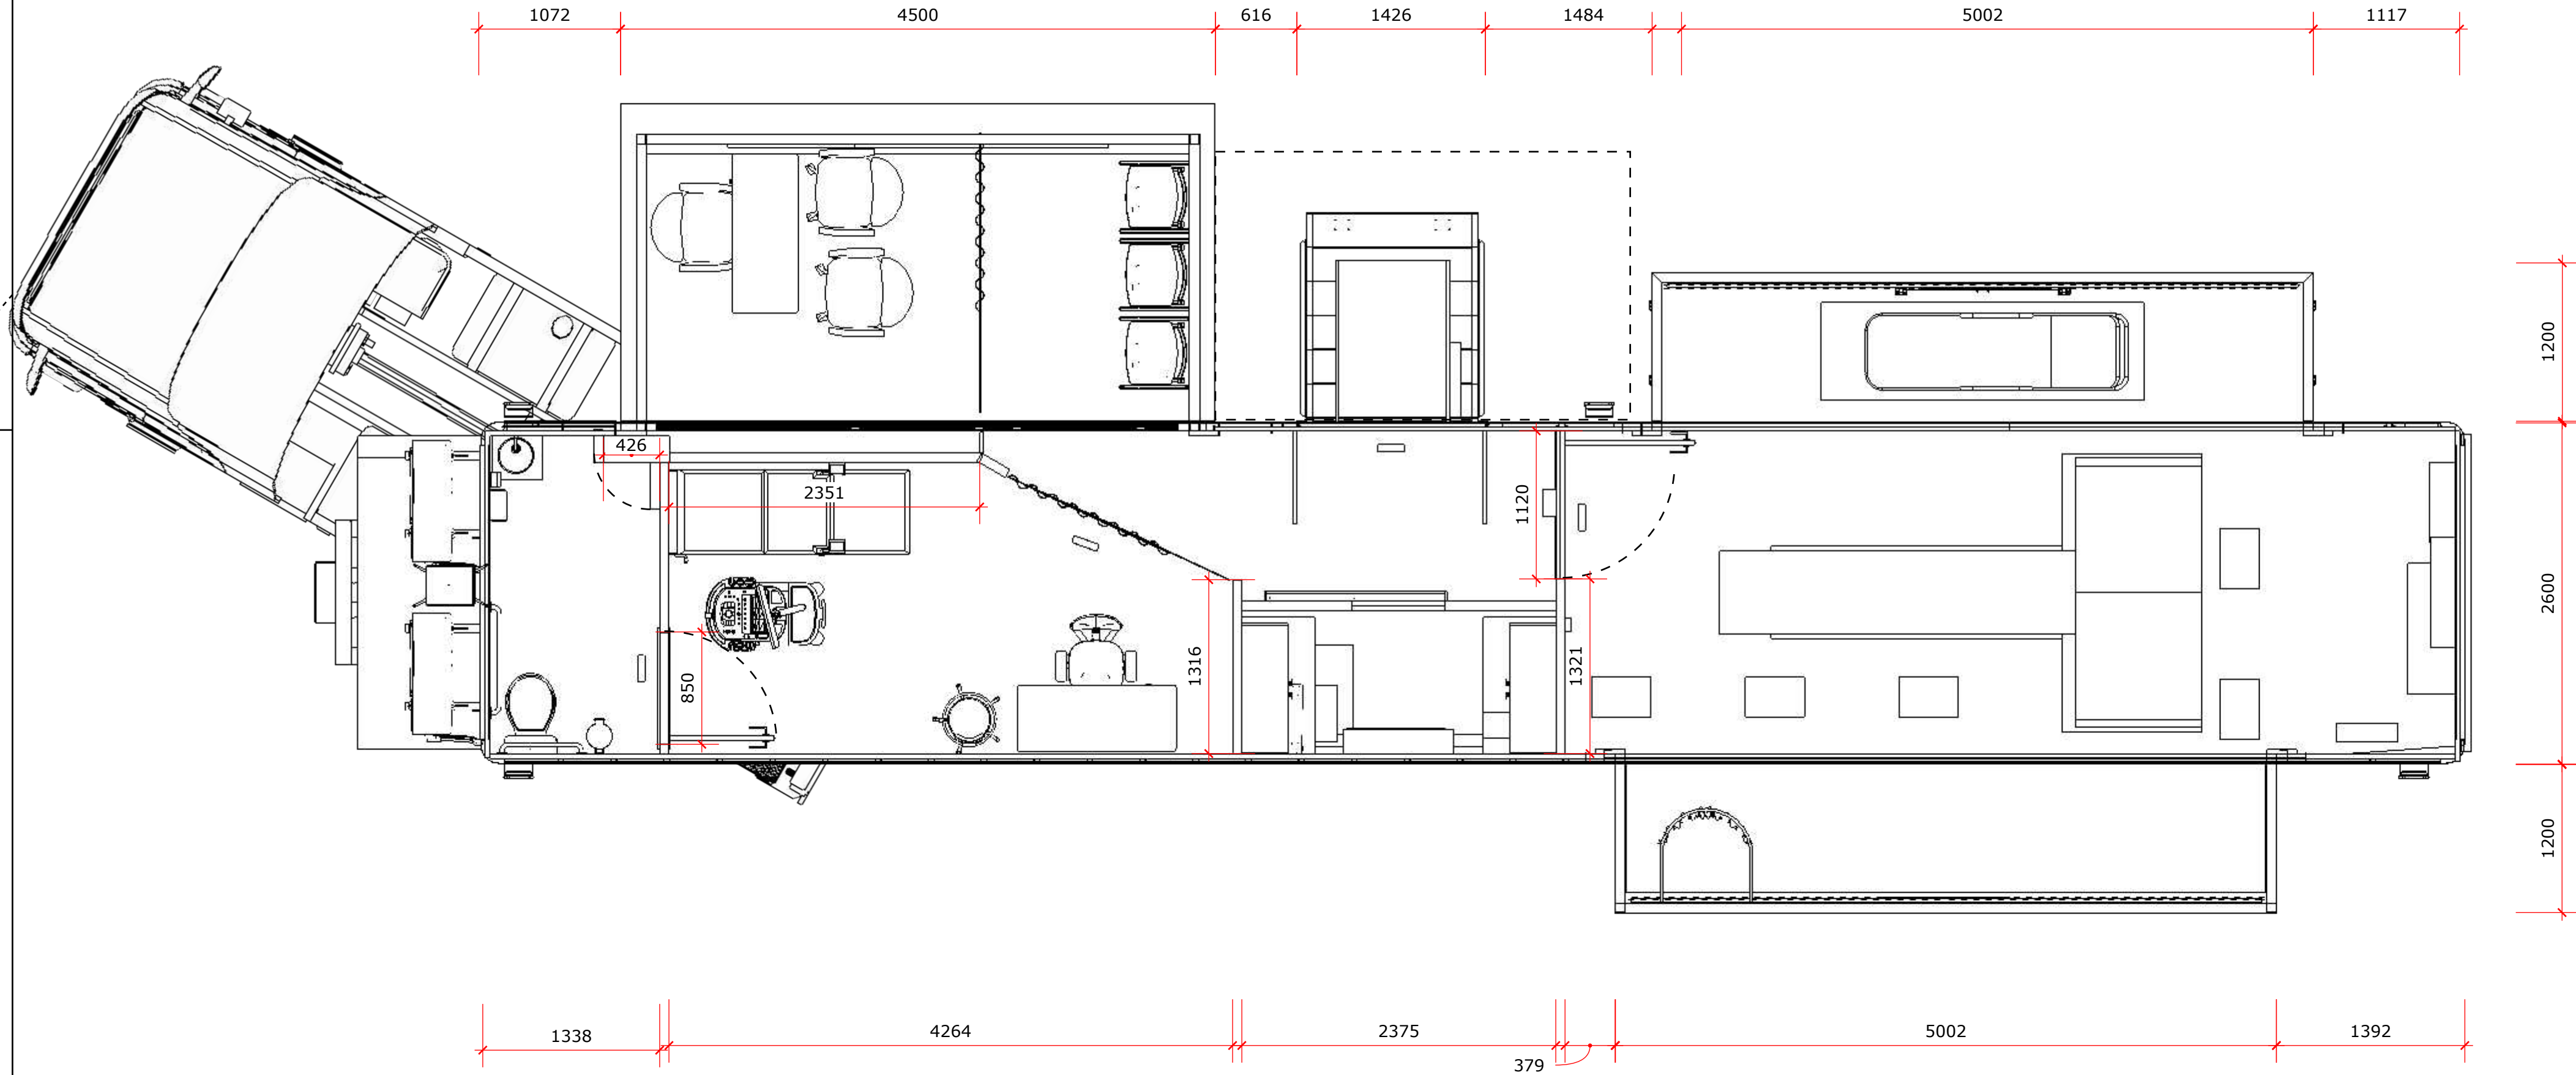

2 PLANTA BAIXA
1:35


FASE	REVISÃO	DATA	DESCRIÇÃO DA REVISÃO	
PE	R00	20/07/2026	INICIAL	
OBS:				
Pedido:	15741	Ref. Comercial:	0.0.2026.1.7.4.AA	2
Projeto:	360	Cliente:	BLUE HEALTH	
Arquivo:	PE-15741-R00	Aplicação:	DETALHAMENTO	17
		Escala:	1:40	
		Projetista:	Karla Souza	
		Aprovação:	Victor Dariano	
		Data:	20 / 07 / 2026	

2 PLANTA BAIXA
1:35

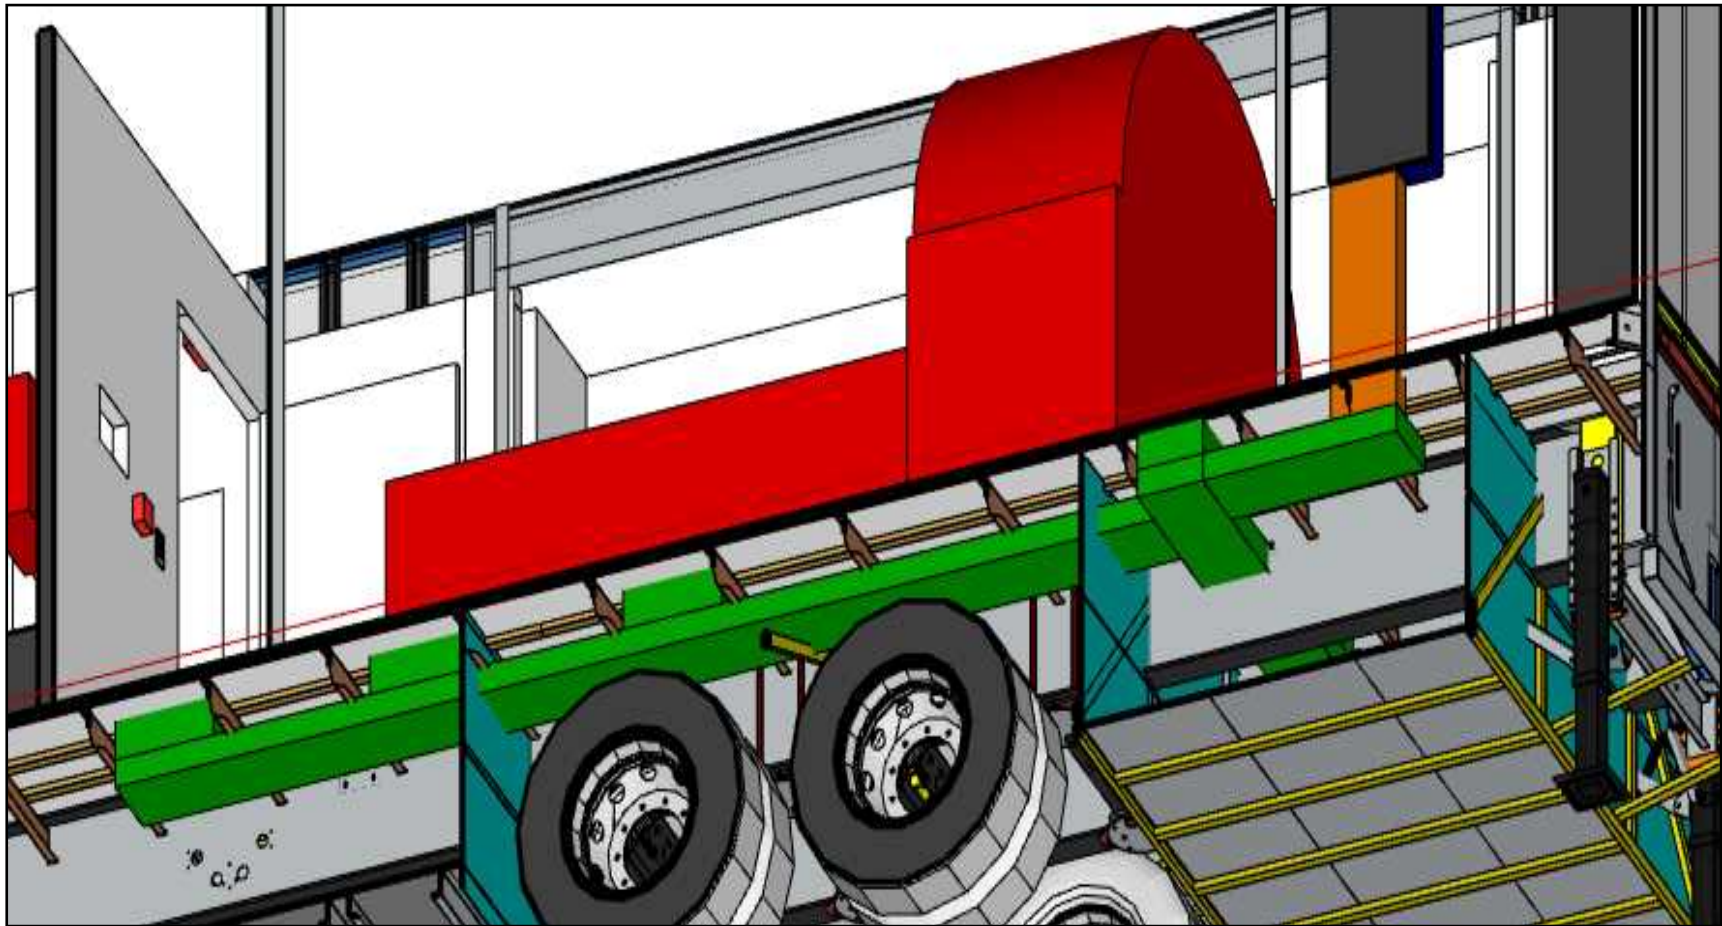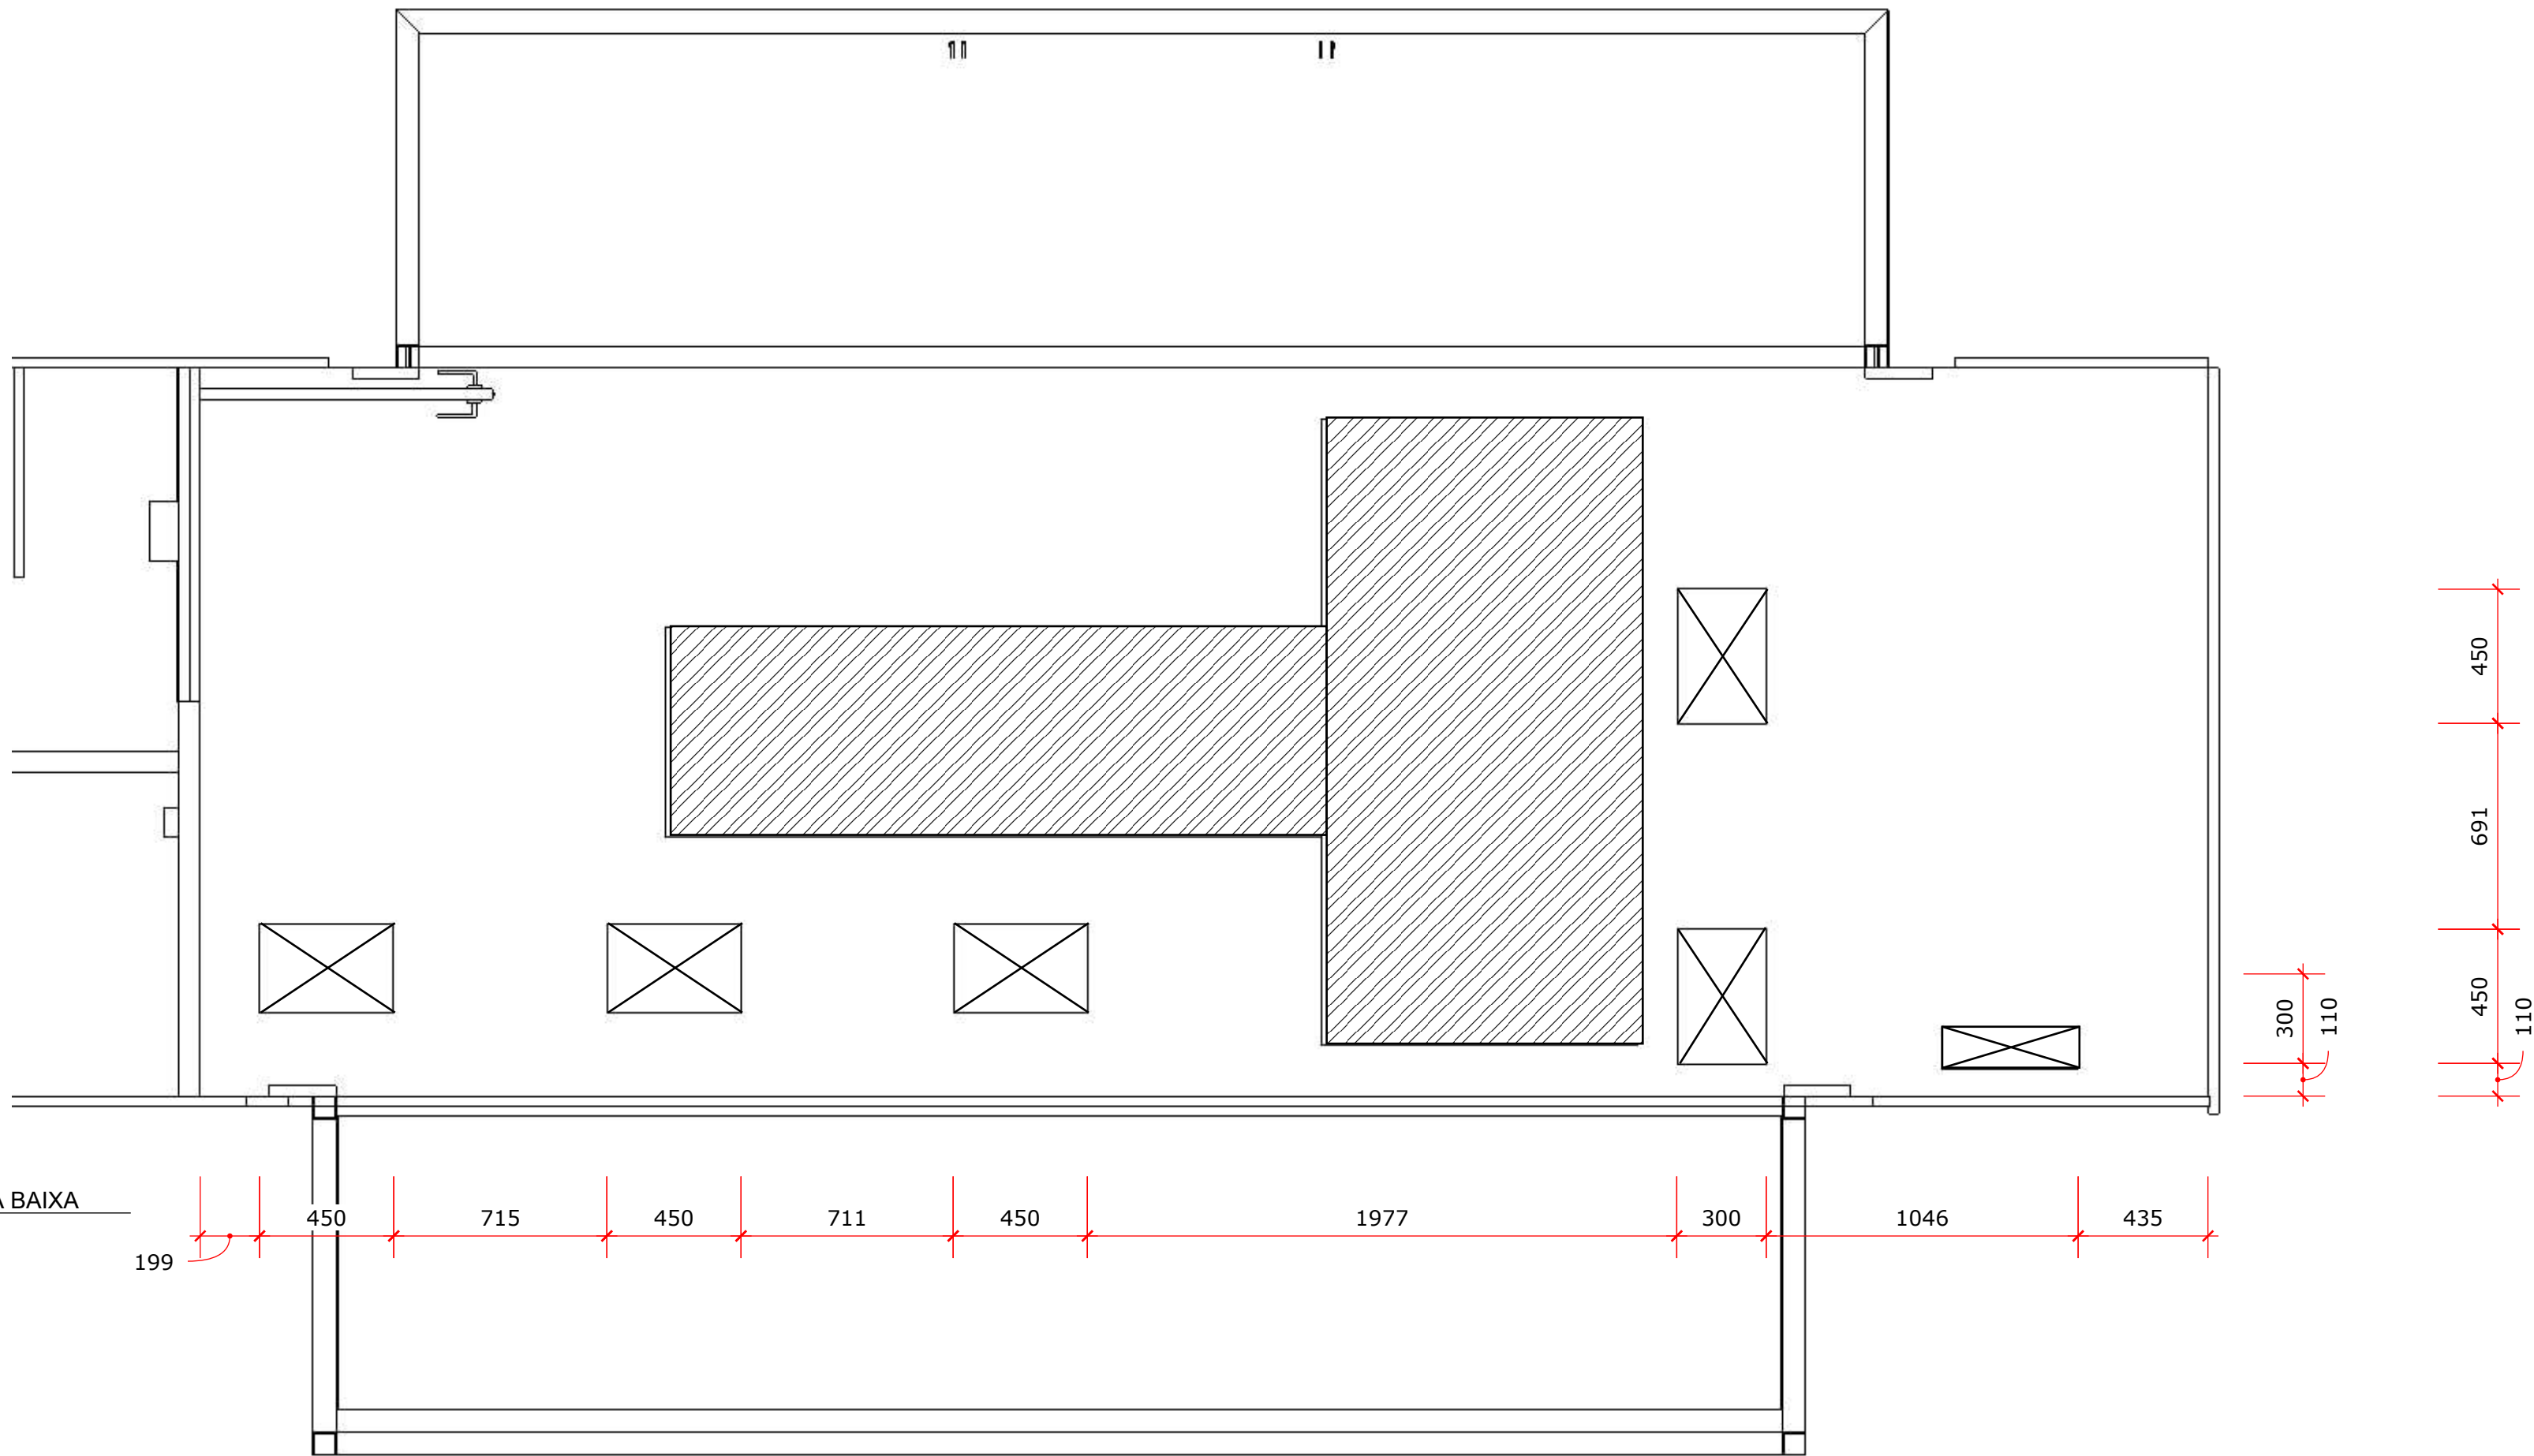


FASE	REVISÃO	DATA	DESCRIÇÃO DA REVISÃO	
PE	R00	20/07/2026	INICIAL	
OBS:				
Pedido:	15741	Ref. Comercial:	0.0.2026.1.7.4.AA	3
Projeto:	360	Cliente:	BLUE HEALTH	
Arquivo:	PE-15741-R00	Aplicação:	CALHA	17
		Escala:	1:40	
		Projetista:	Karla Souza	
		Aprovação:	Victor Dariano	
		Data:	20 / 07 / 2026	



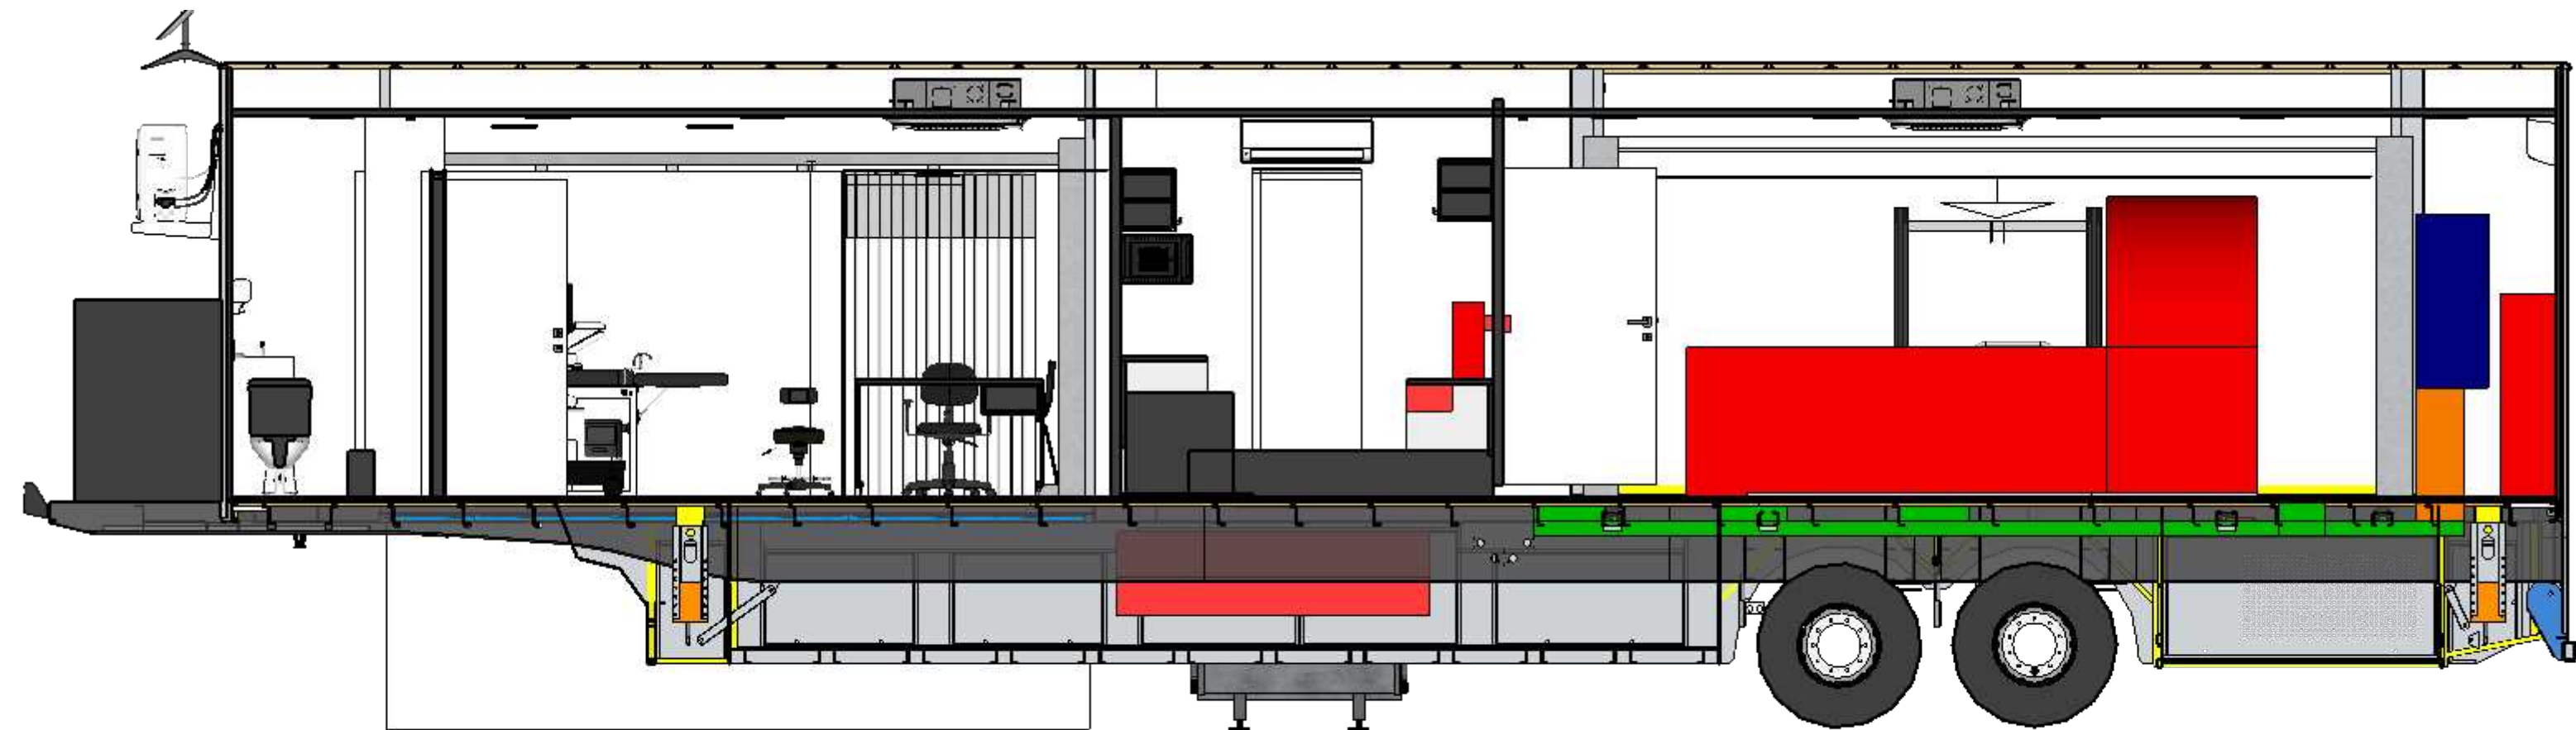


3 LATERAL ESQUERDA
1:40

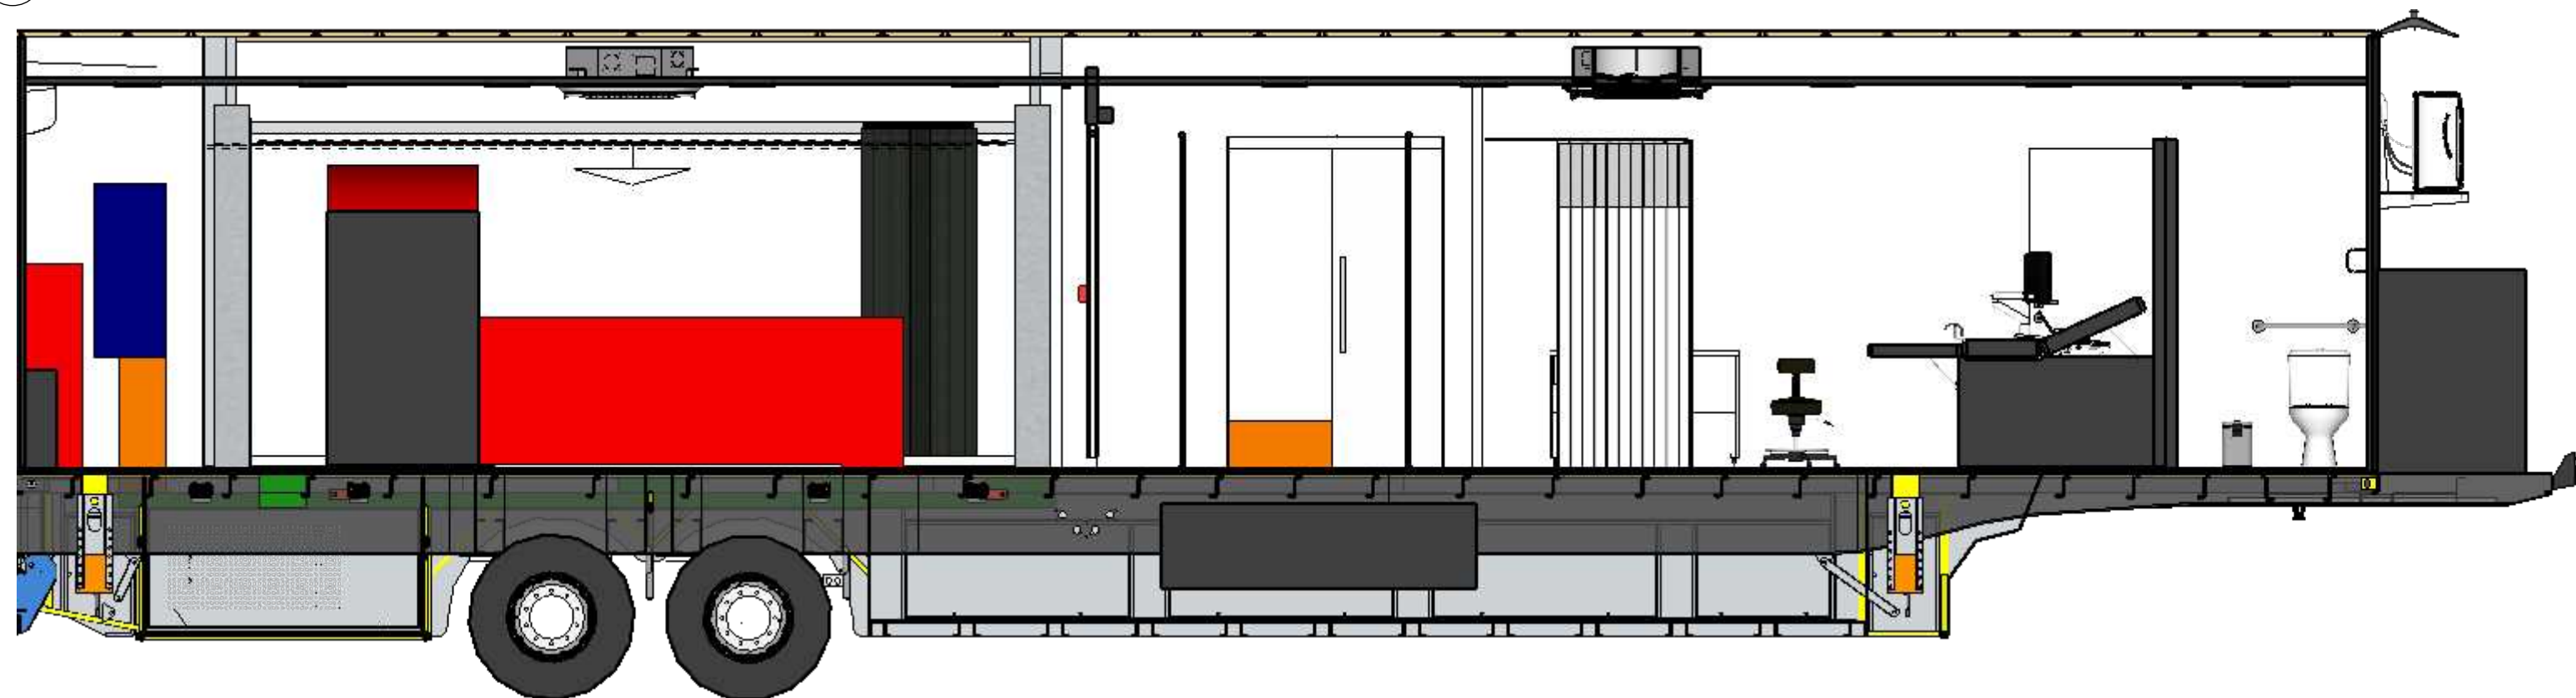

4 LATERAL DIREITA
1:40


FASE	REVISÃO	DATA	DESCRIÇÃO DA REVISÃO	
PE	R00	20/07/2026	INICIAL	
OBS:				
Pedido:	15741	Ref. Comercial:	0.0.2026.1.7.4.AA	5
Projeto:	360	Cliente:	BLUE HEALTH	
Arquivo:	PE-15741-R00	Aplicação:	CORTES	17
		Escala:	1:40	
		Projetista:	Karla Souza	
		Aprovação:	Victor Dariano	
		Data:	20 / 07 / 2026	

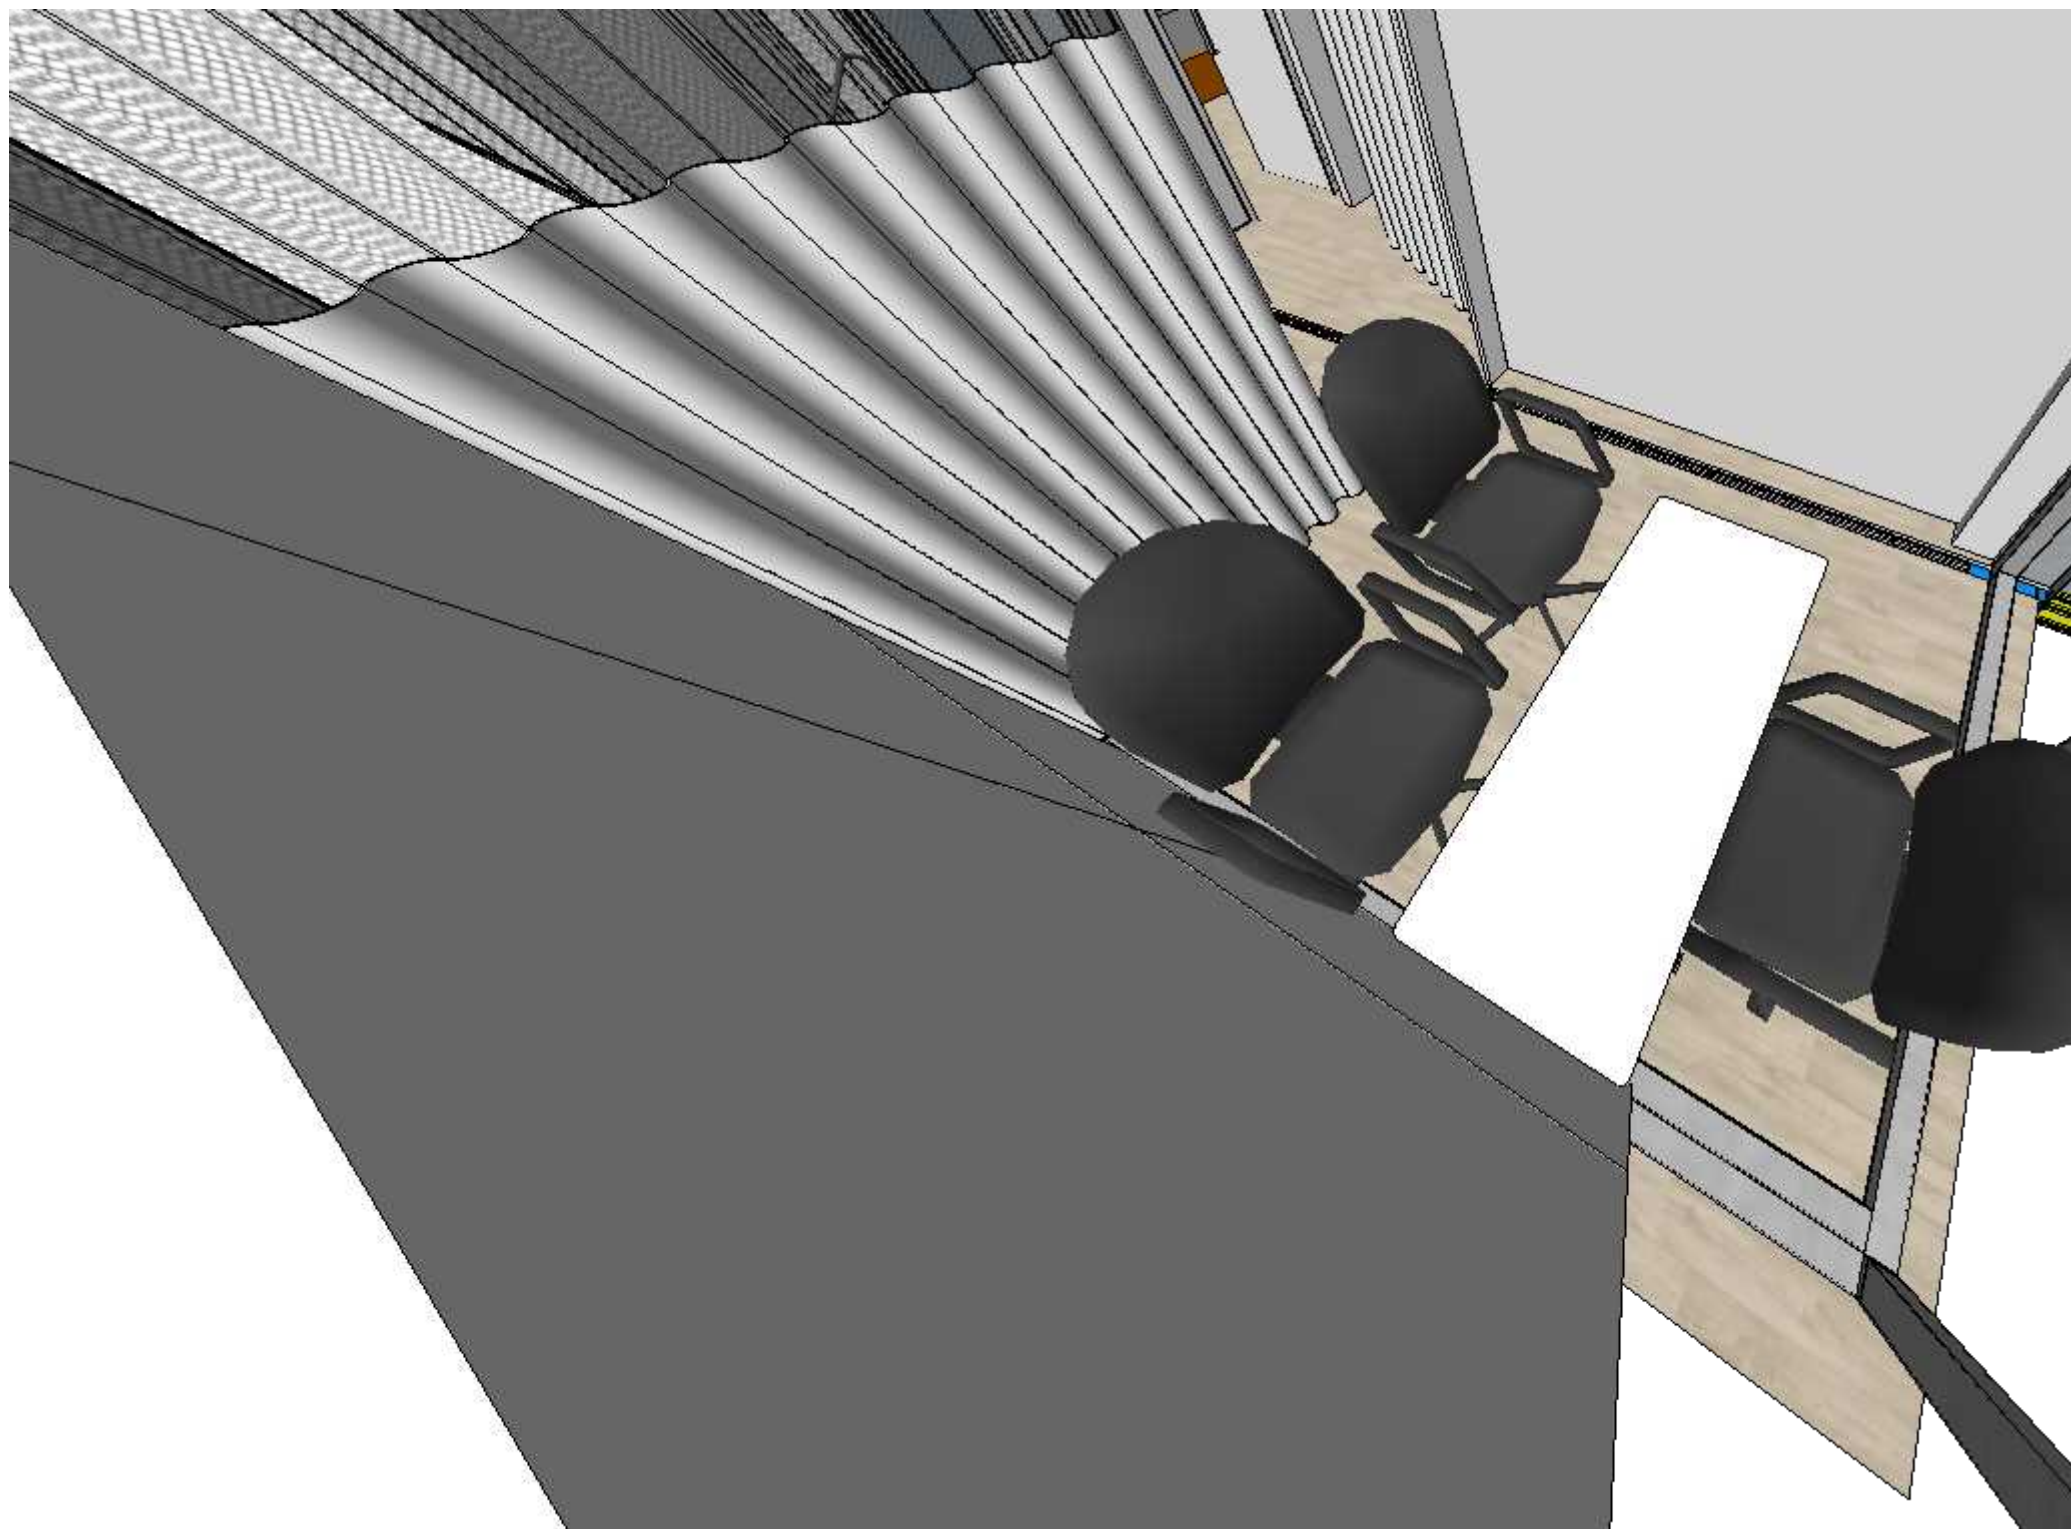

5 PERSPECTIVA 1



6 PERSPECTIVA 2

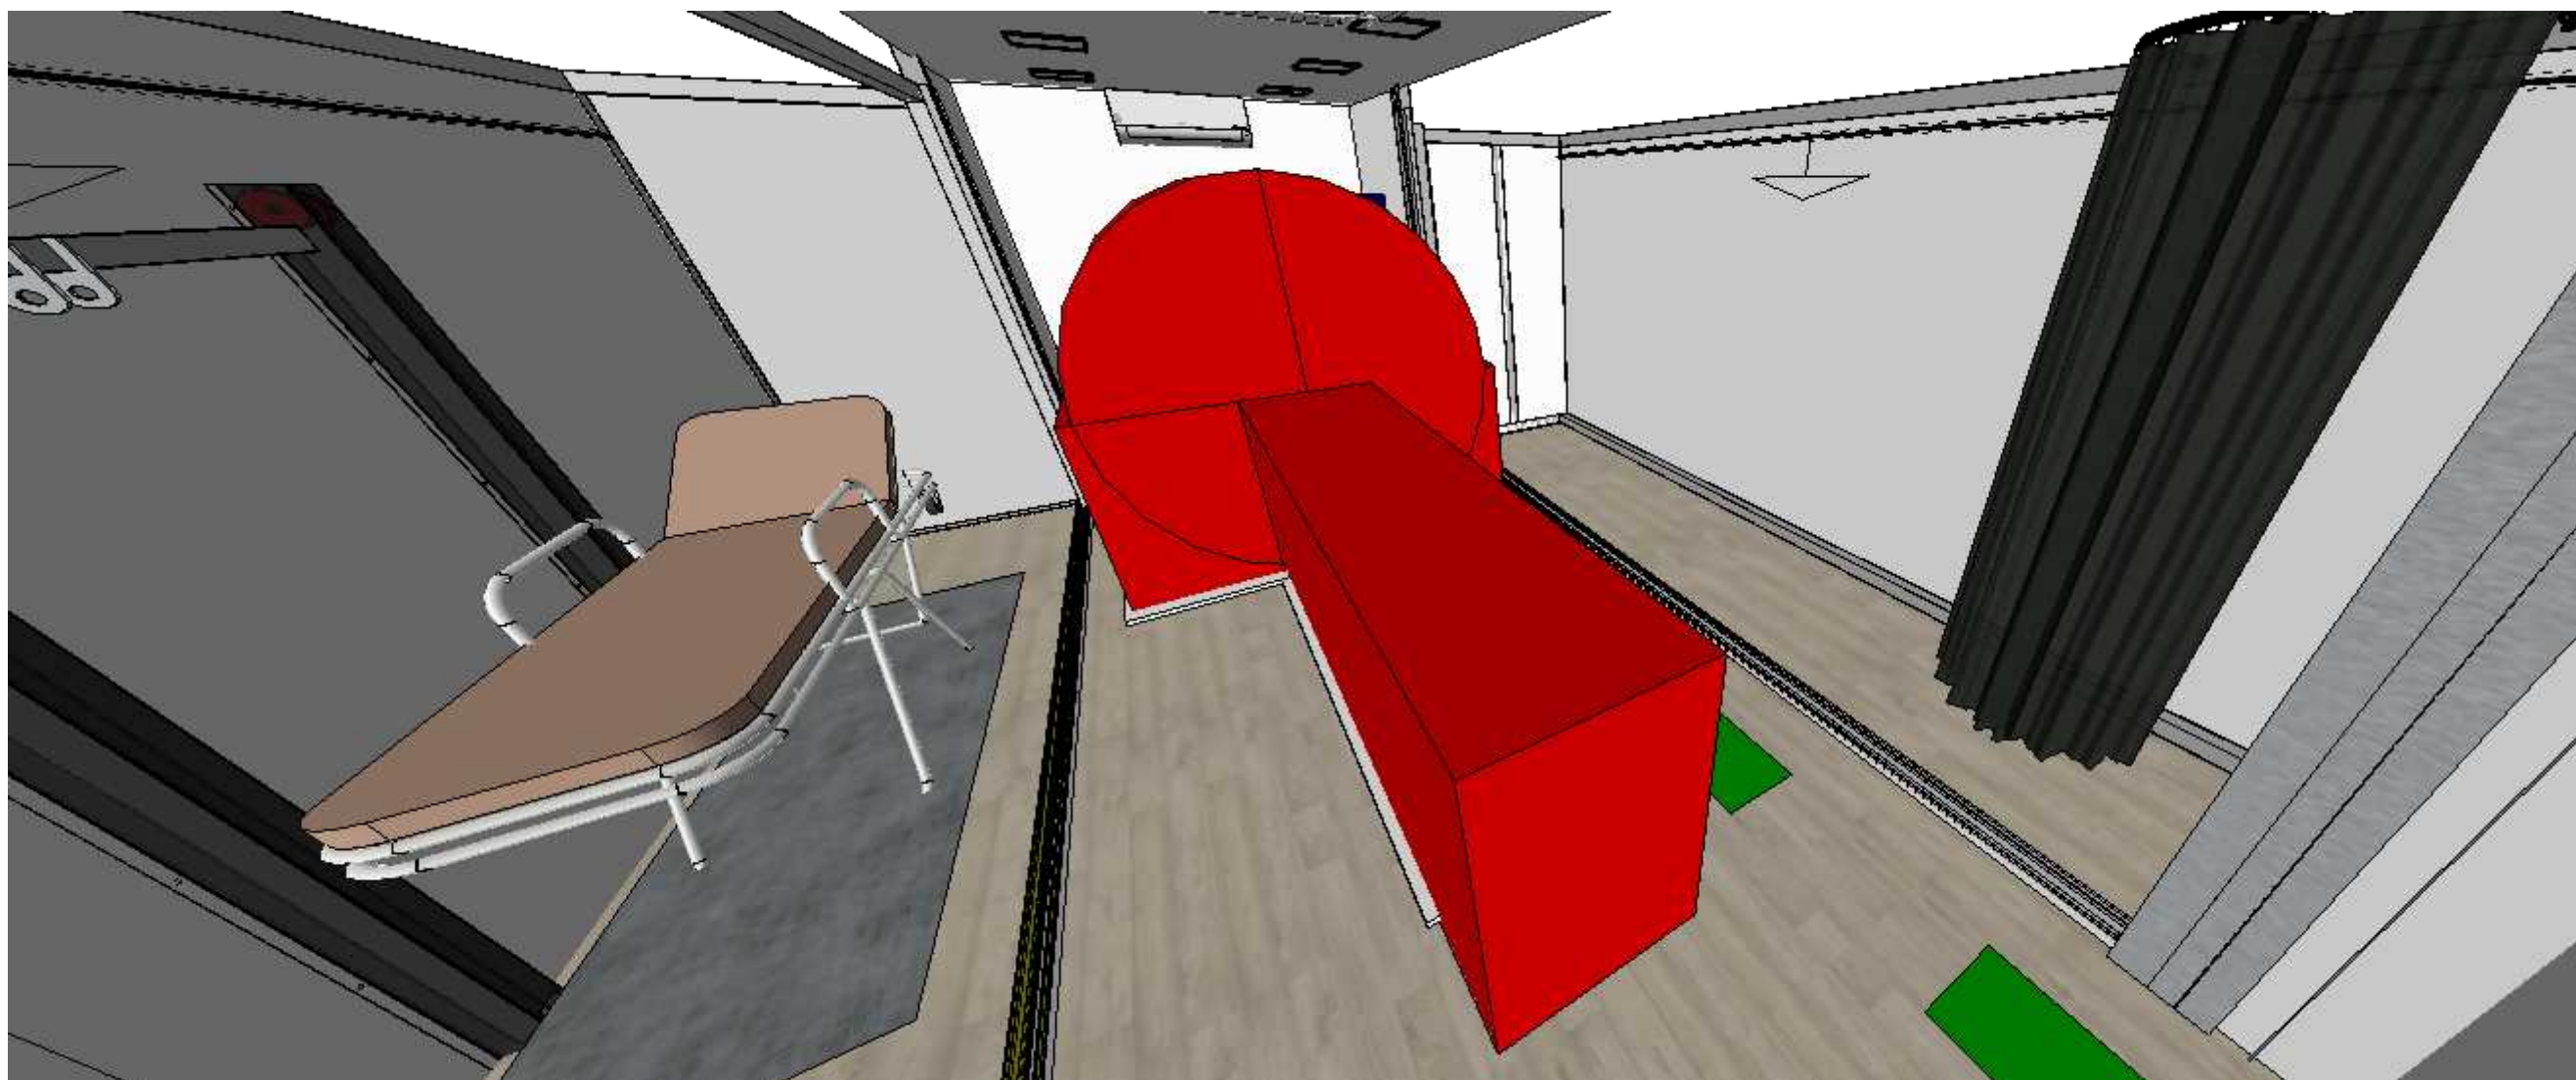


7 PERSPECTIVA 3


FASE	REVISÃO	DATA	DESCRIÇÃO DA REVISÃO	
PE	R00	20/07/2026	INICIAL	
OBS:				
Pedido:	15741	Ref. Comercial:	0.0.2026.1.7.4.AA	6
Projeto:	360	Cliente:	BLUE HEALTH	
Arquivo:	PE-15741-R00	Aplicação:	PERSPECTIVAS	17
		Escala:	1:40	
		Projetista:	Karla Souza	
		Aprovação:	Victor Dariano	
		Data:	20 / 07 / 2026	




8 LATERAL ESQUERDA
1:40

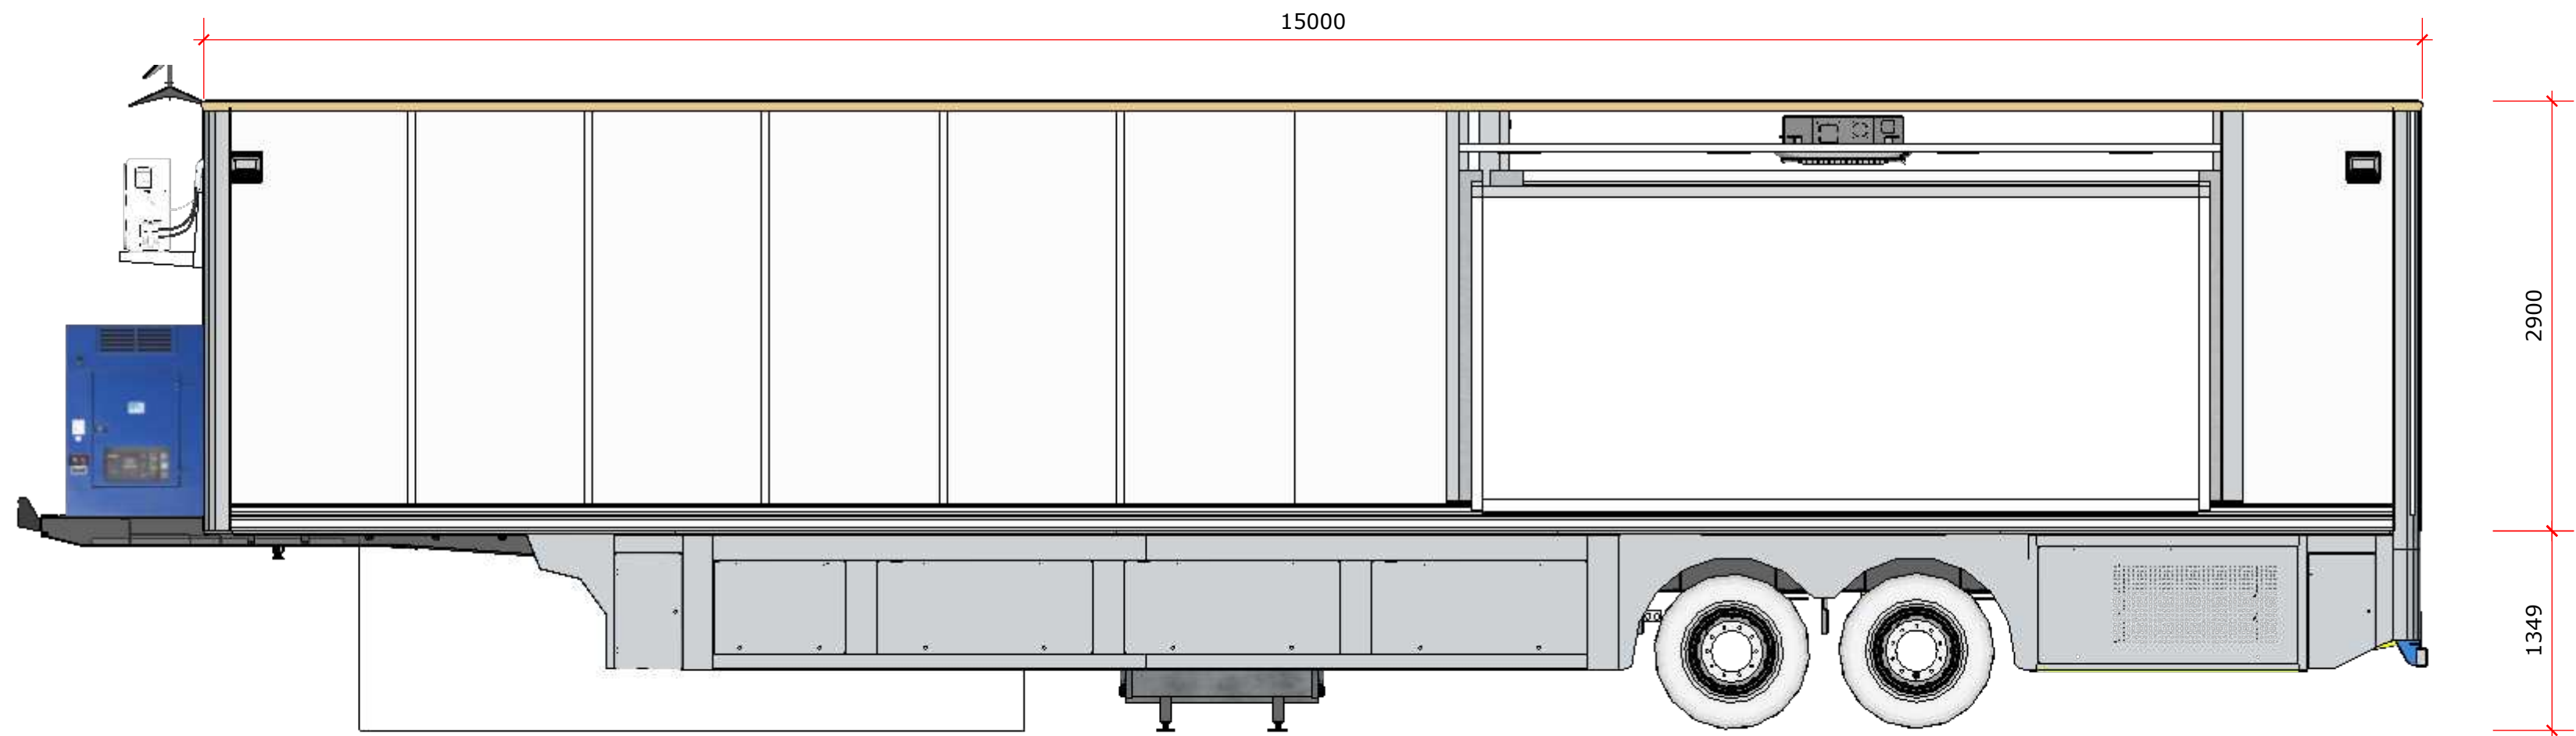

9 LATERAL DIREITA
1:40

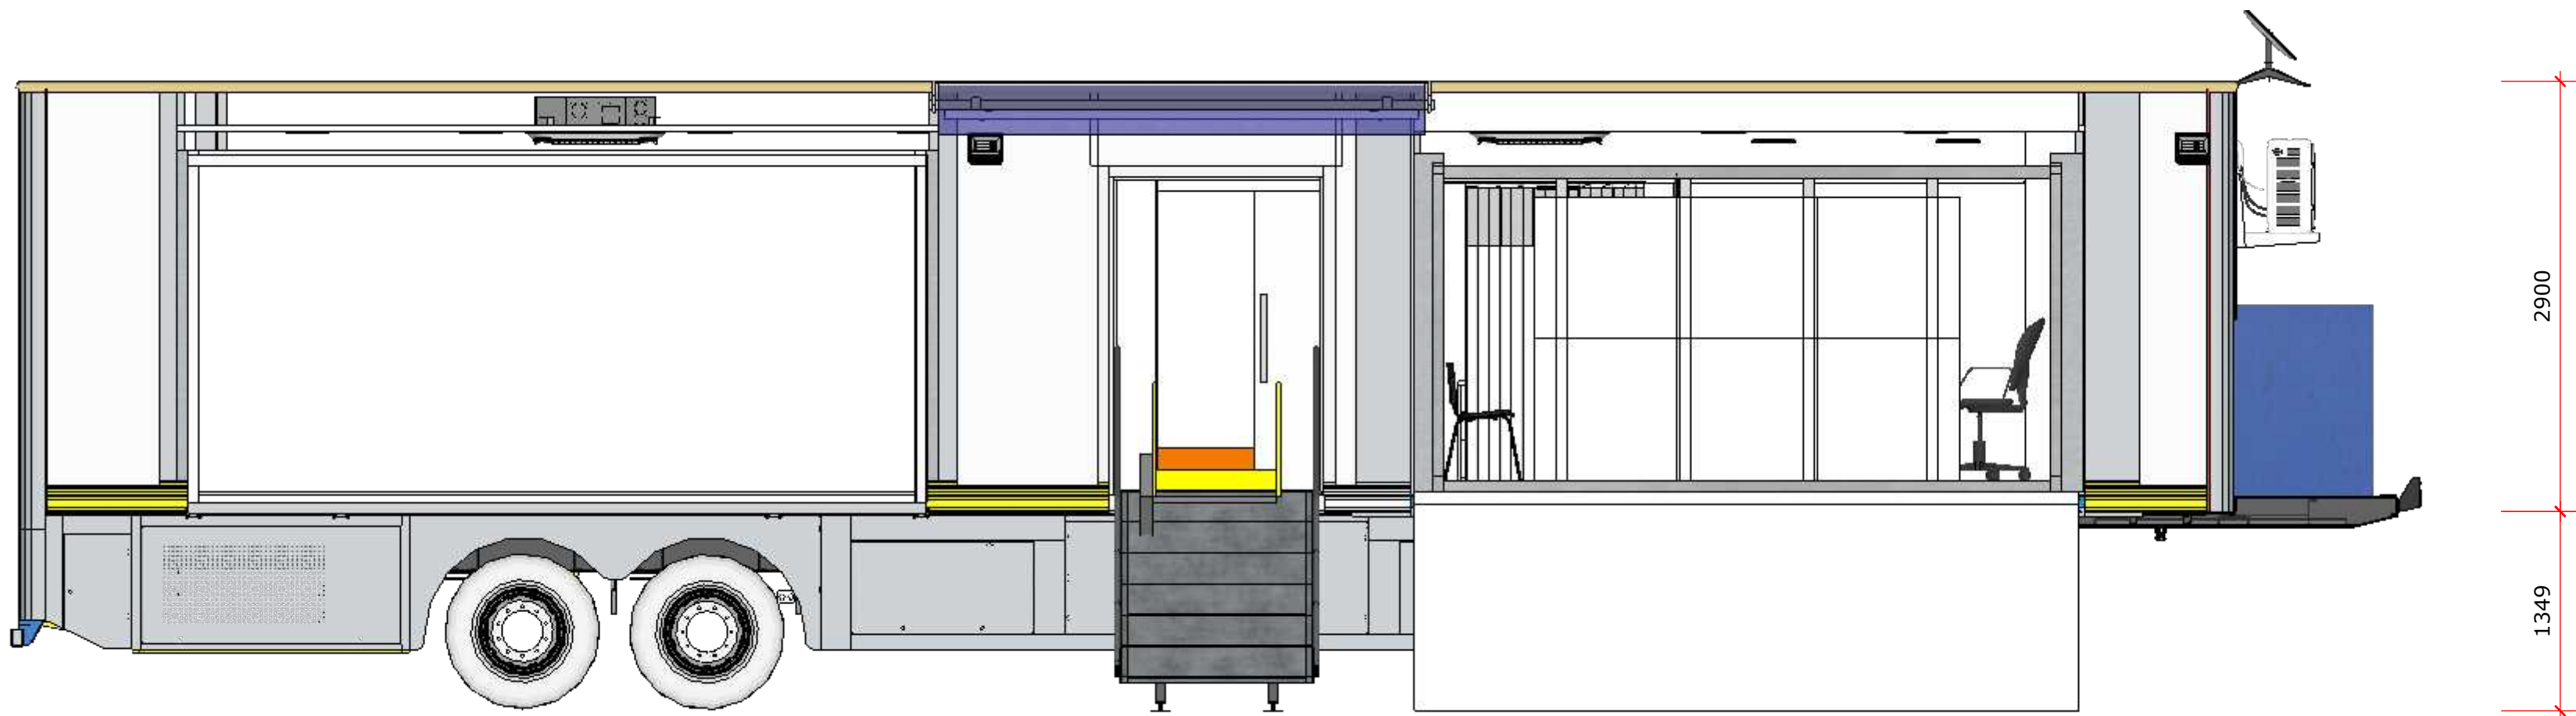


10 TRASEIRA
1:40

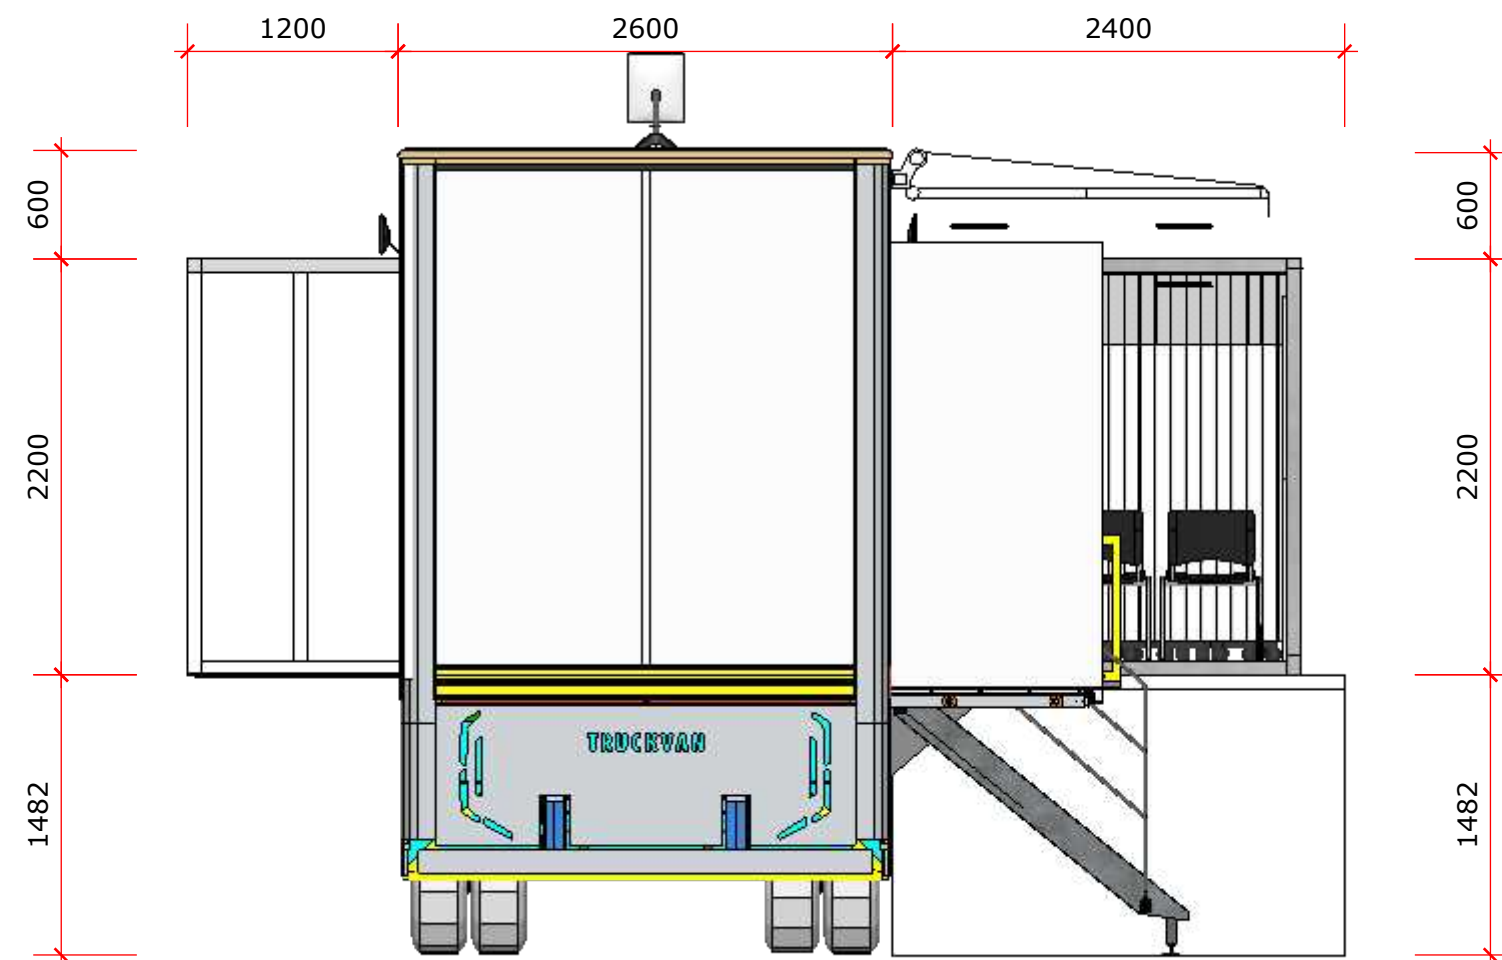


FASE	REVISÃO	DATA	DESCRIÇÃO DA REVISÃO	
PE	R00	20/07/2026	INICIAL	
OBS:				
Pedido:	15741	Ref. Comercial:	0.0.2026.1.7.4.AA	7
Projeto:	360	Cliente:	BLUE HEALTH	
Arquivo:	PE-15741-R00	Aplicação:	CONJUNTO GERAL	17
		Escala:	1:40	
		Projetista:	Karla Souza	
		Aprovação:	Victor Dariano	
		Data:	20 / 07 / 2026	


8 LATERAL ESQUERDA
1:40

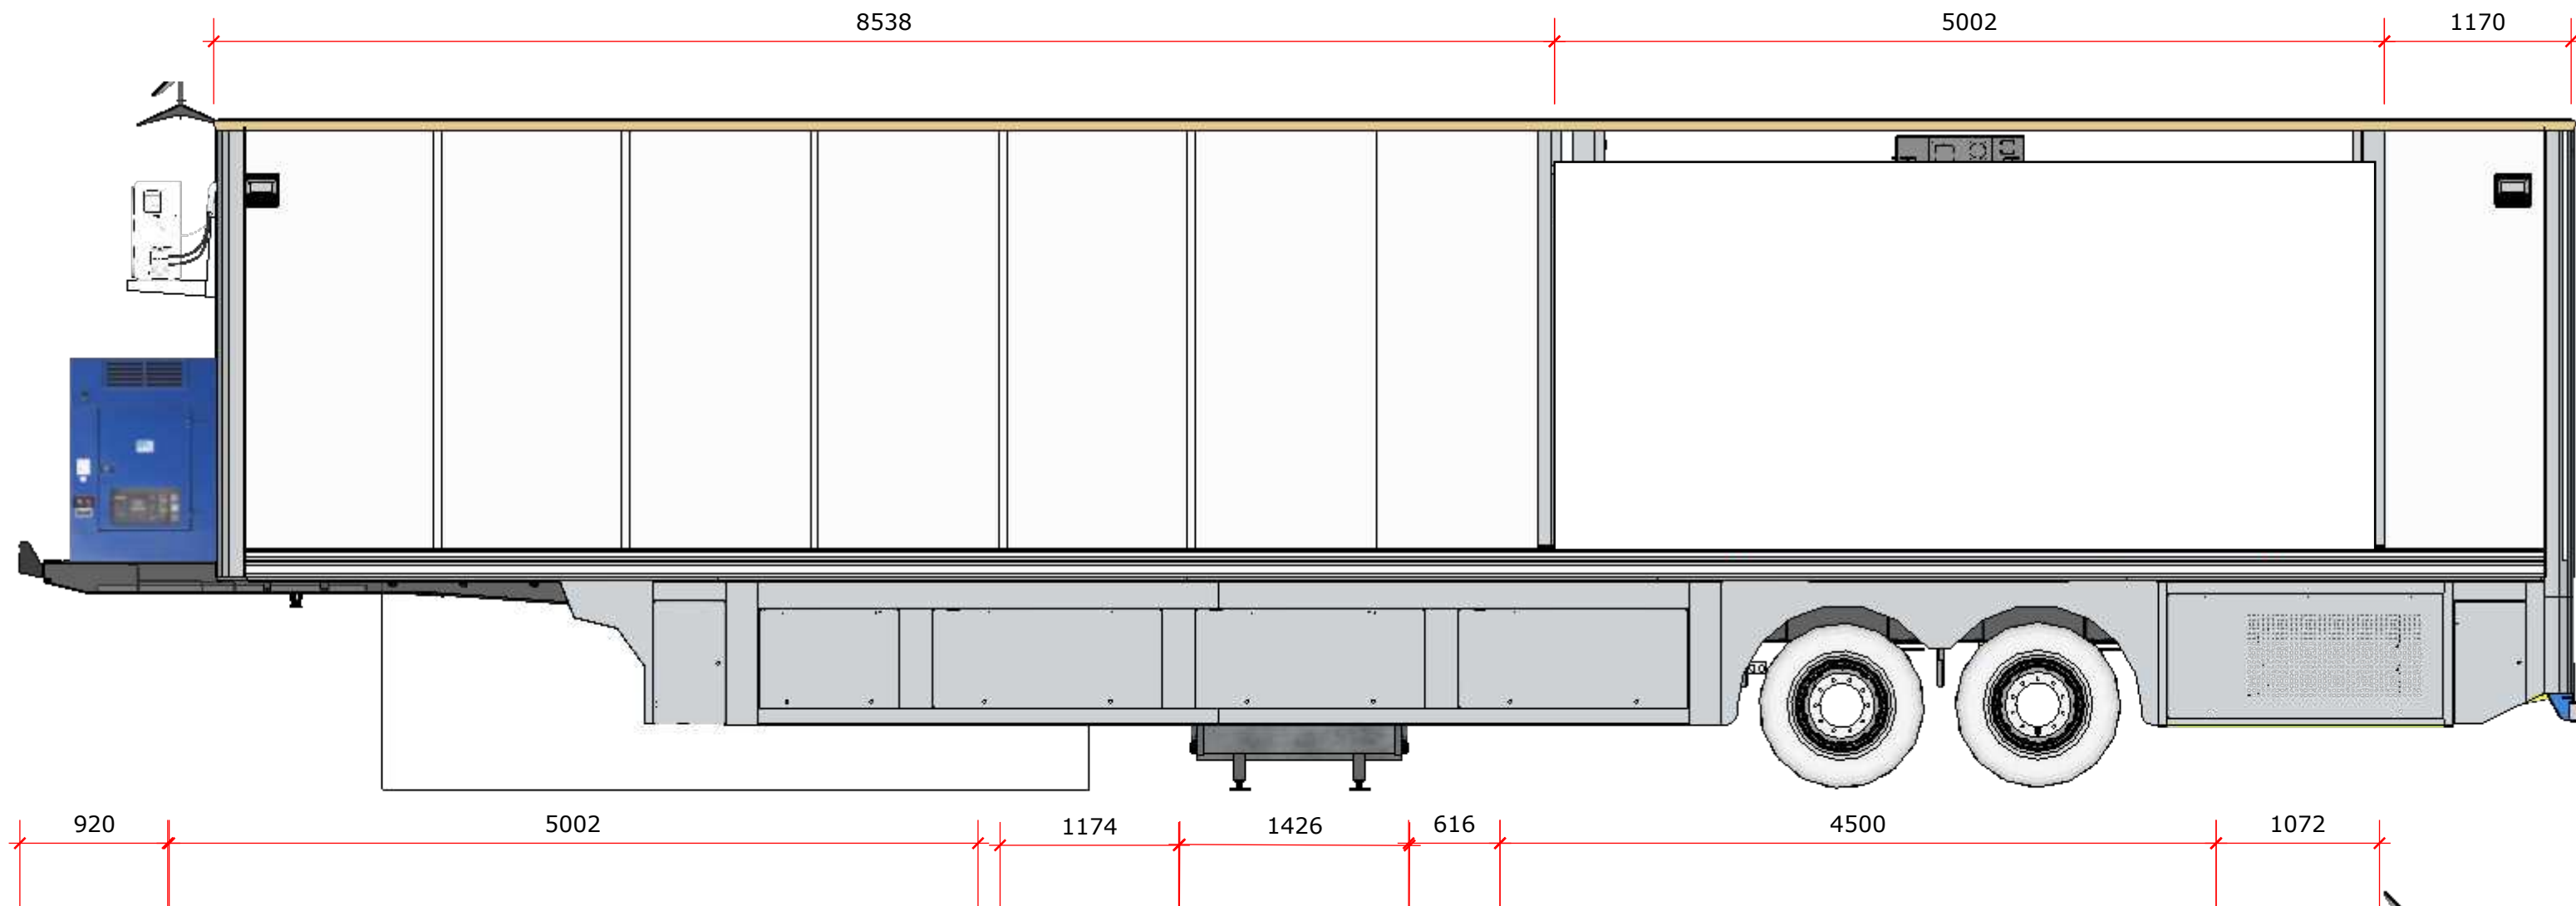


9 LATERAL DIREITA
1:40

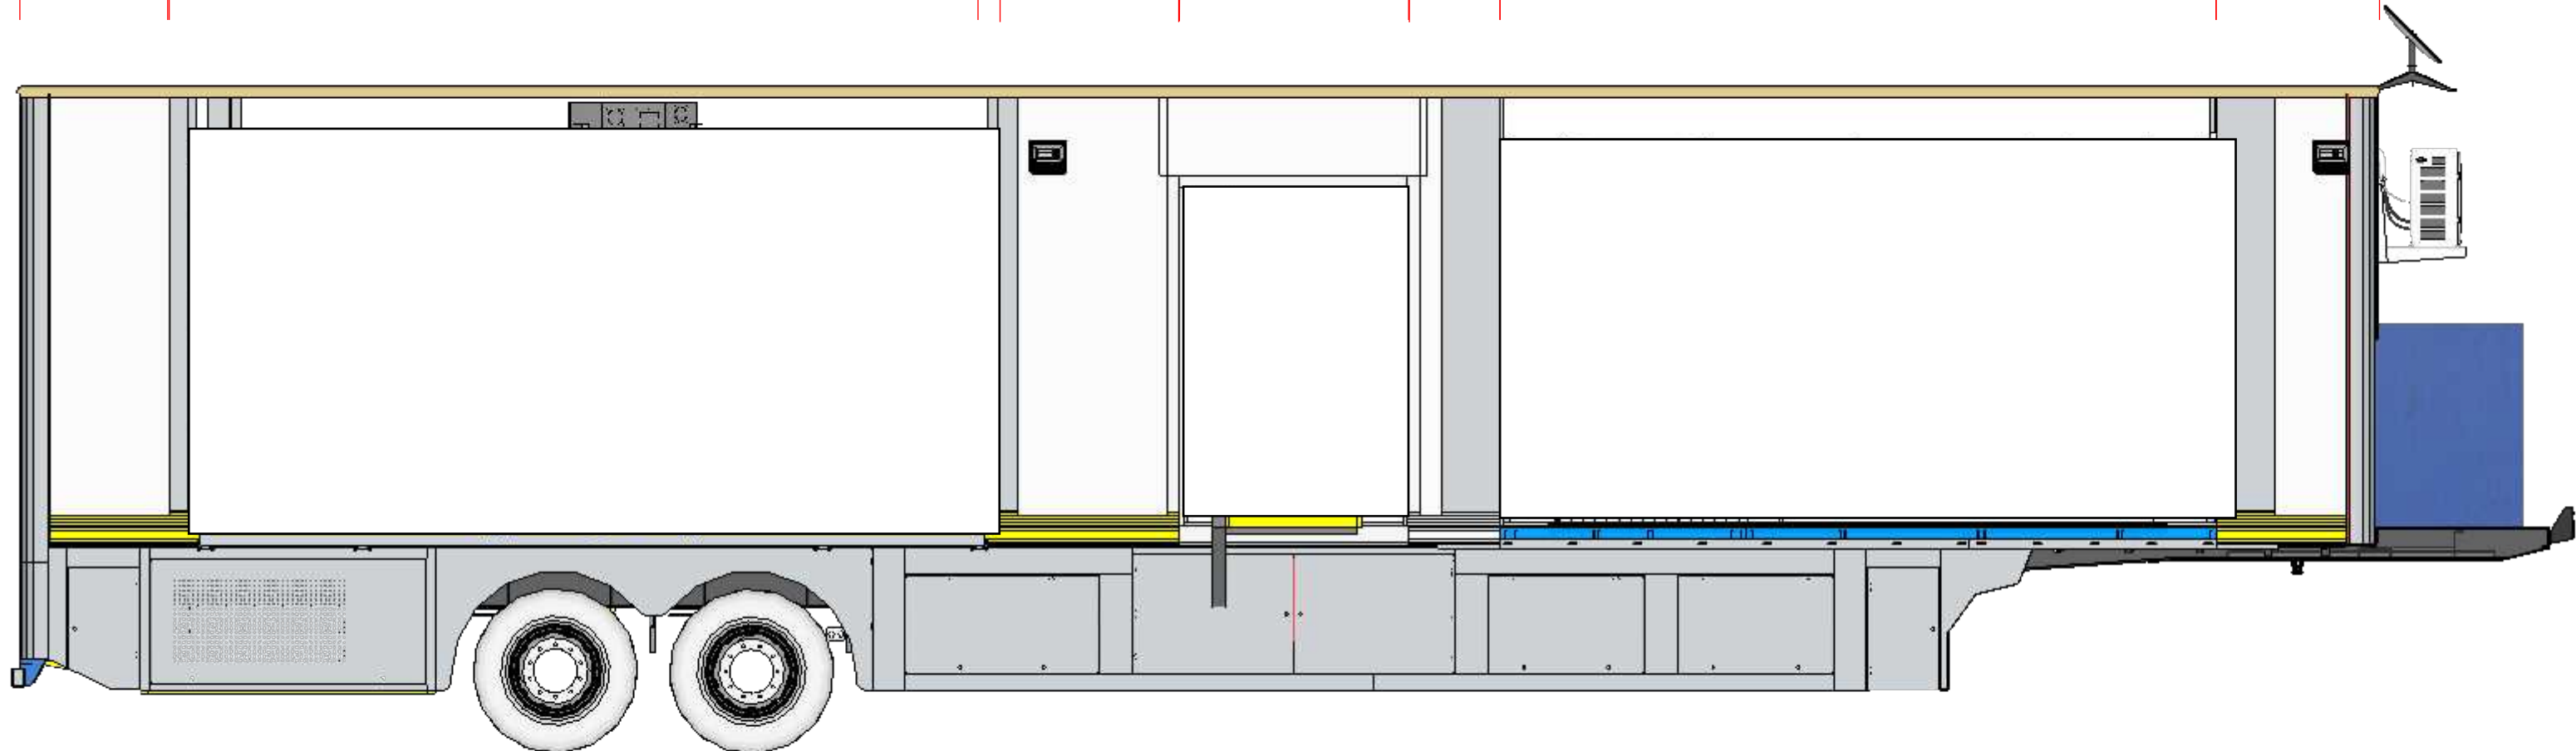

10 TRASEIRA
1:40

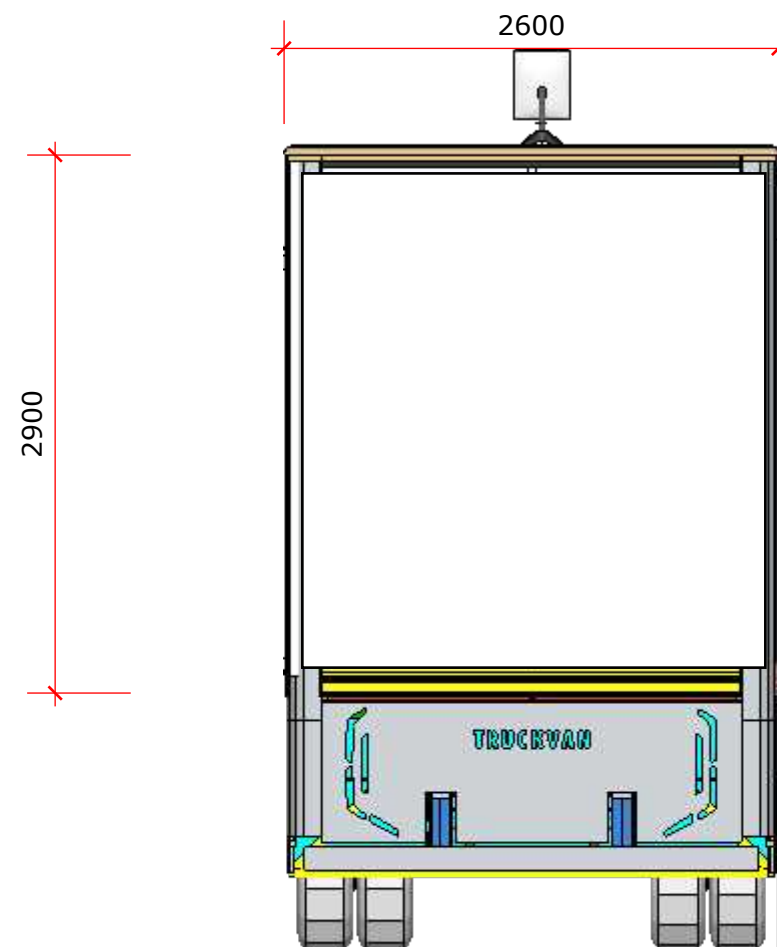

FASE	REVISÃO	DATA	DESCRIÇÃO DA REVISÃO	
PE	R00	20/07/2026	INICIAL	
OBS:				
Pedido:	15741	Ref. Comercial:	0.0.2026.1.7.4.AA	8
Projeto:	360	Cliente:	BLUE HEALTH	
Arquivo:	PE-15741-R00	Aplicação:	PROJETO VISUAL	17
		Escala:	1:40	
		Projetista:	Karla Souza	
		Aprovação:	Victor Dariano	
		Data:	20 / 07 / 2026	

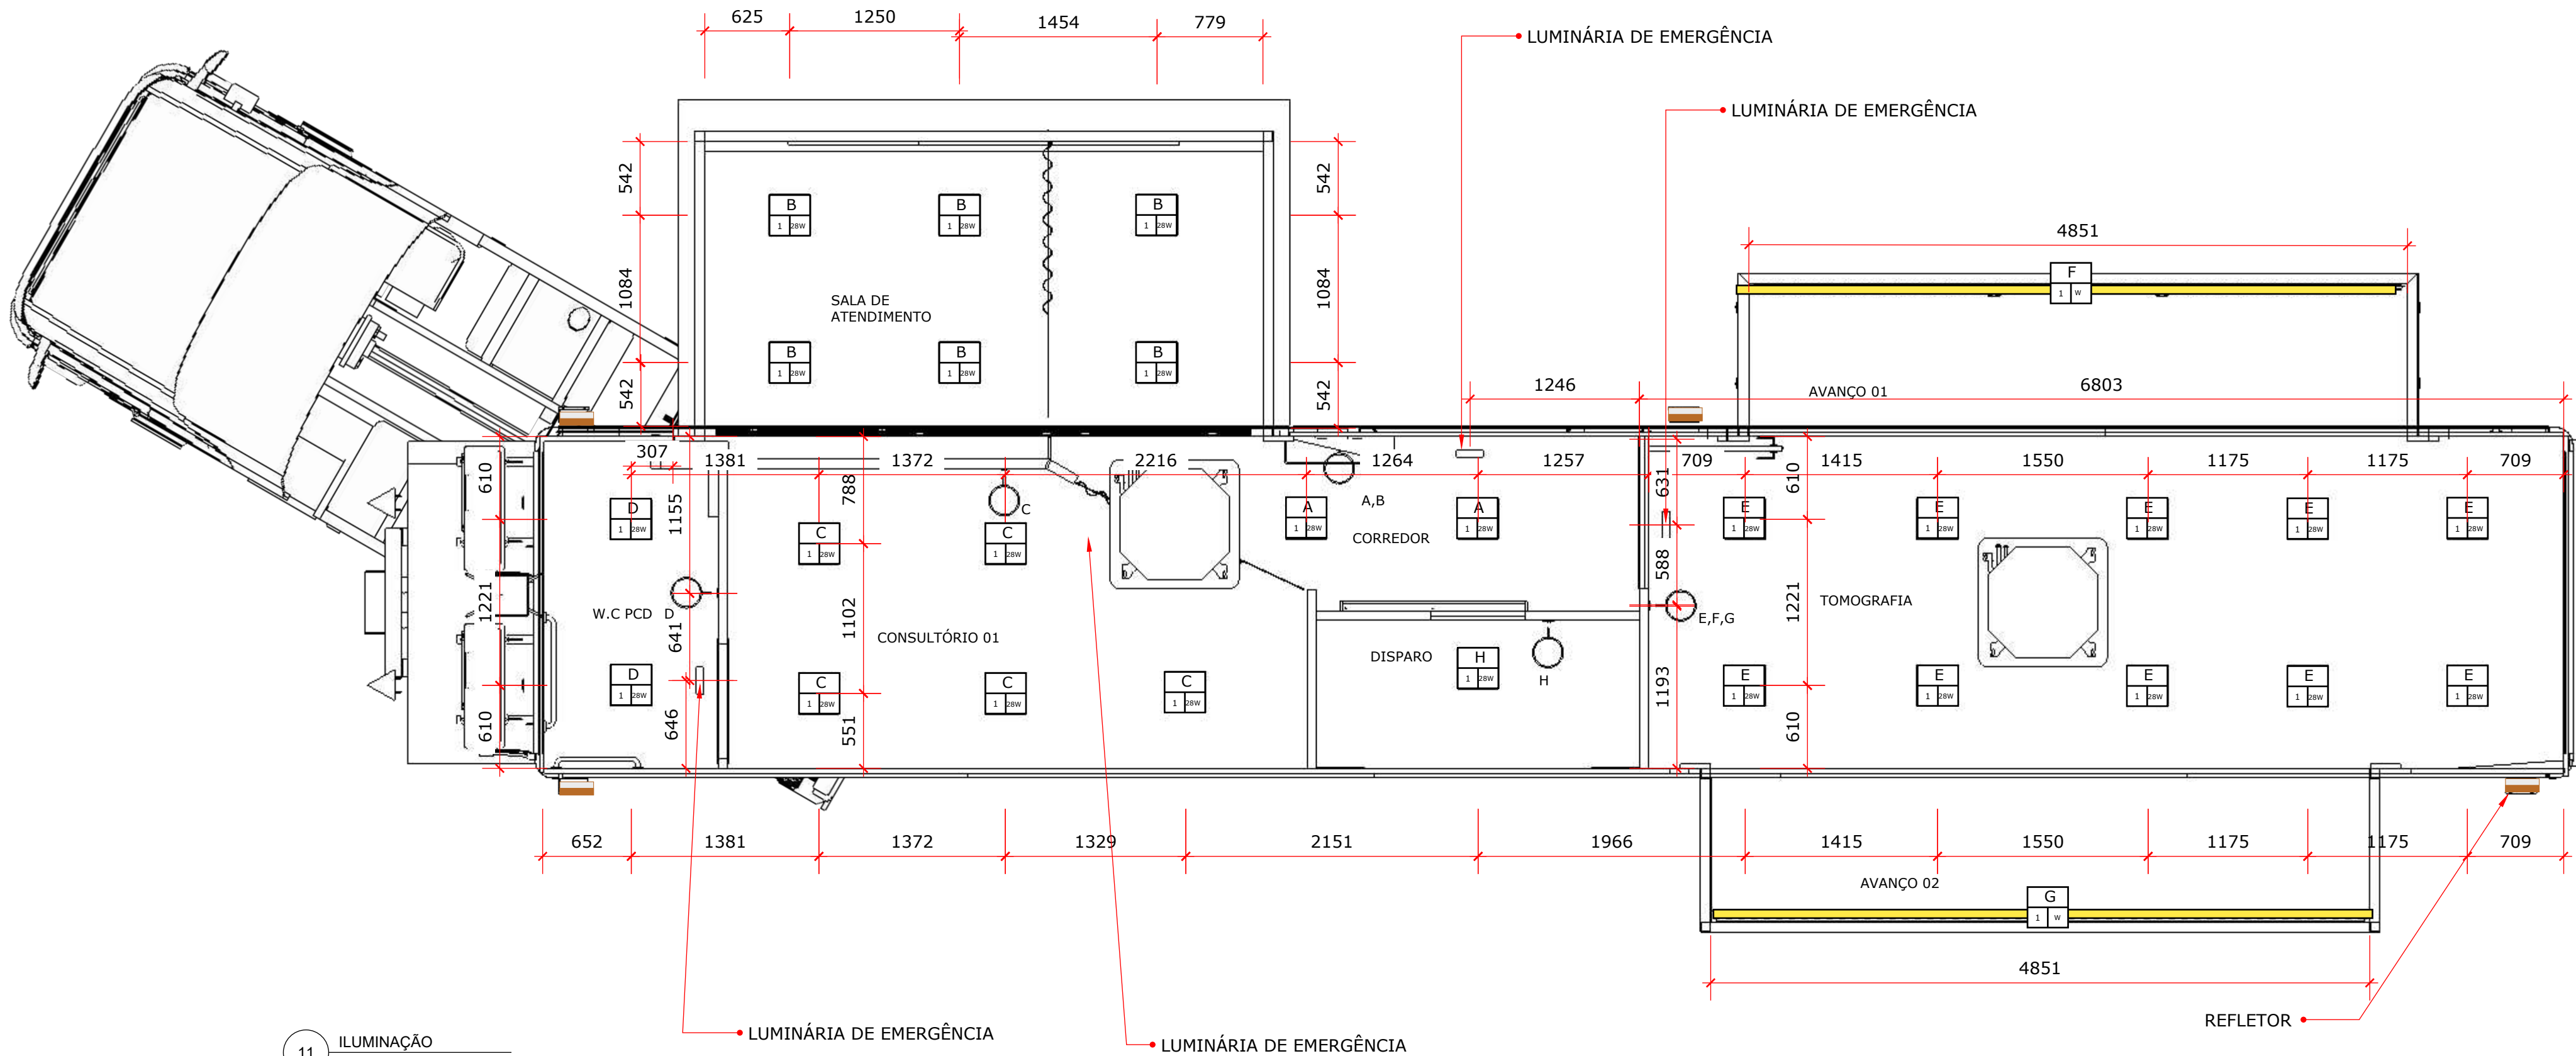


11 ILUMINAÇÃO
1:35

VERIFICAR MEDIDAS NO LOCAL


INTERRUPTOR	DESCRIÇÃO	
A	CORREDOR	
B	SALA DE ATENDIMENTO	
C	CONSULTÓRIO 02	
D	W.C PCD	
E	SALA DE TOMOGRAFIA	
F	AVANÇO 01	
G	AVANÇO 02	
H	SALA DE DISPARO	
SIMBOLOGIA	ESPECIFICAÇÕES	
	INTERRUPTOR	
	A - INTERRUPTOR	
	1 - CIRCUITO	
	28W - POTÊNCIA	
	LUMINÁRIA DE EMERGÊNCIA	
	QDL - Quadro Geral	
	REFLETOR	
	FITA DE LED	

TABELA ILUMINAÇÃO					
CÓD	DESCRIÇÃO	QTD.	MEDIDA	INSTALAÇÃO	POTÊNCIA
A	PLAFON QUADRADO DE EMBUTIR 300X300	26	EMBUTIDO NO FORRO	28W	
1	LUMINÁRIAS DE EMERGÊNCIA	2	EMBUTIDO NO FORRO	3W	
2	LUMINÁRIA TARTARUGA	2	MALEIRO	6W	
3	REFLETOR LED	4	EXTERNO	100W	
4	FITA DE LED	2	EMBUTIDO NO FORRO		

FASE	REVISÃO	DATA	DESCRIÇÃO DA REVISÃO	
PE	R00	20/07/2026	INICIAL	
OBS:				
Pedido:	15741	Ref. Comercial:	0.0.2026.1.7.4.AA	9
Projeto:	360	Cliente:	BLUE HEALTH	
Arquivo:	PE-15741-R00	Aplicação:	ILUMINAÇÃO	
		Escala:	1:40	17
		Projetista:	Karla Souza	
		Aprovação:	Victor Dariano	
		Data:	20 / 07 / 2026	

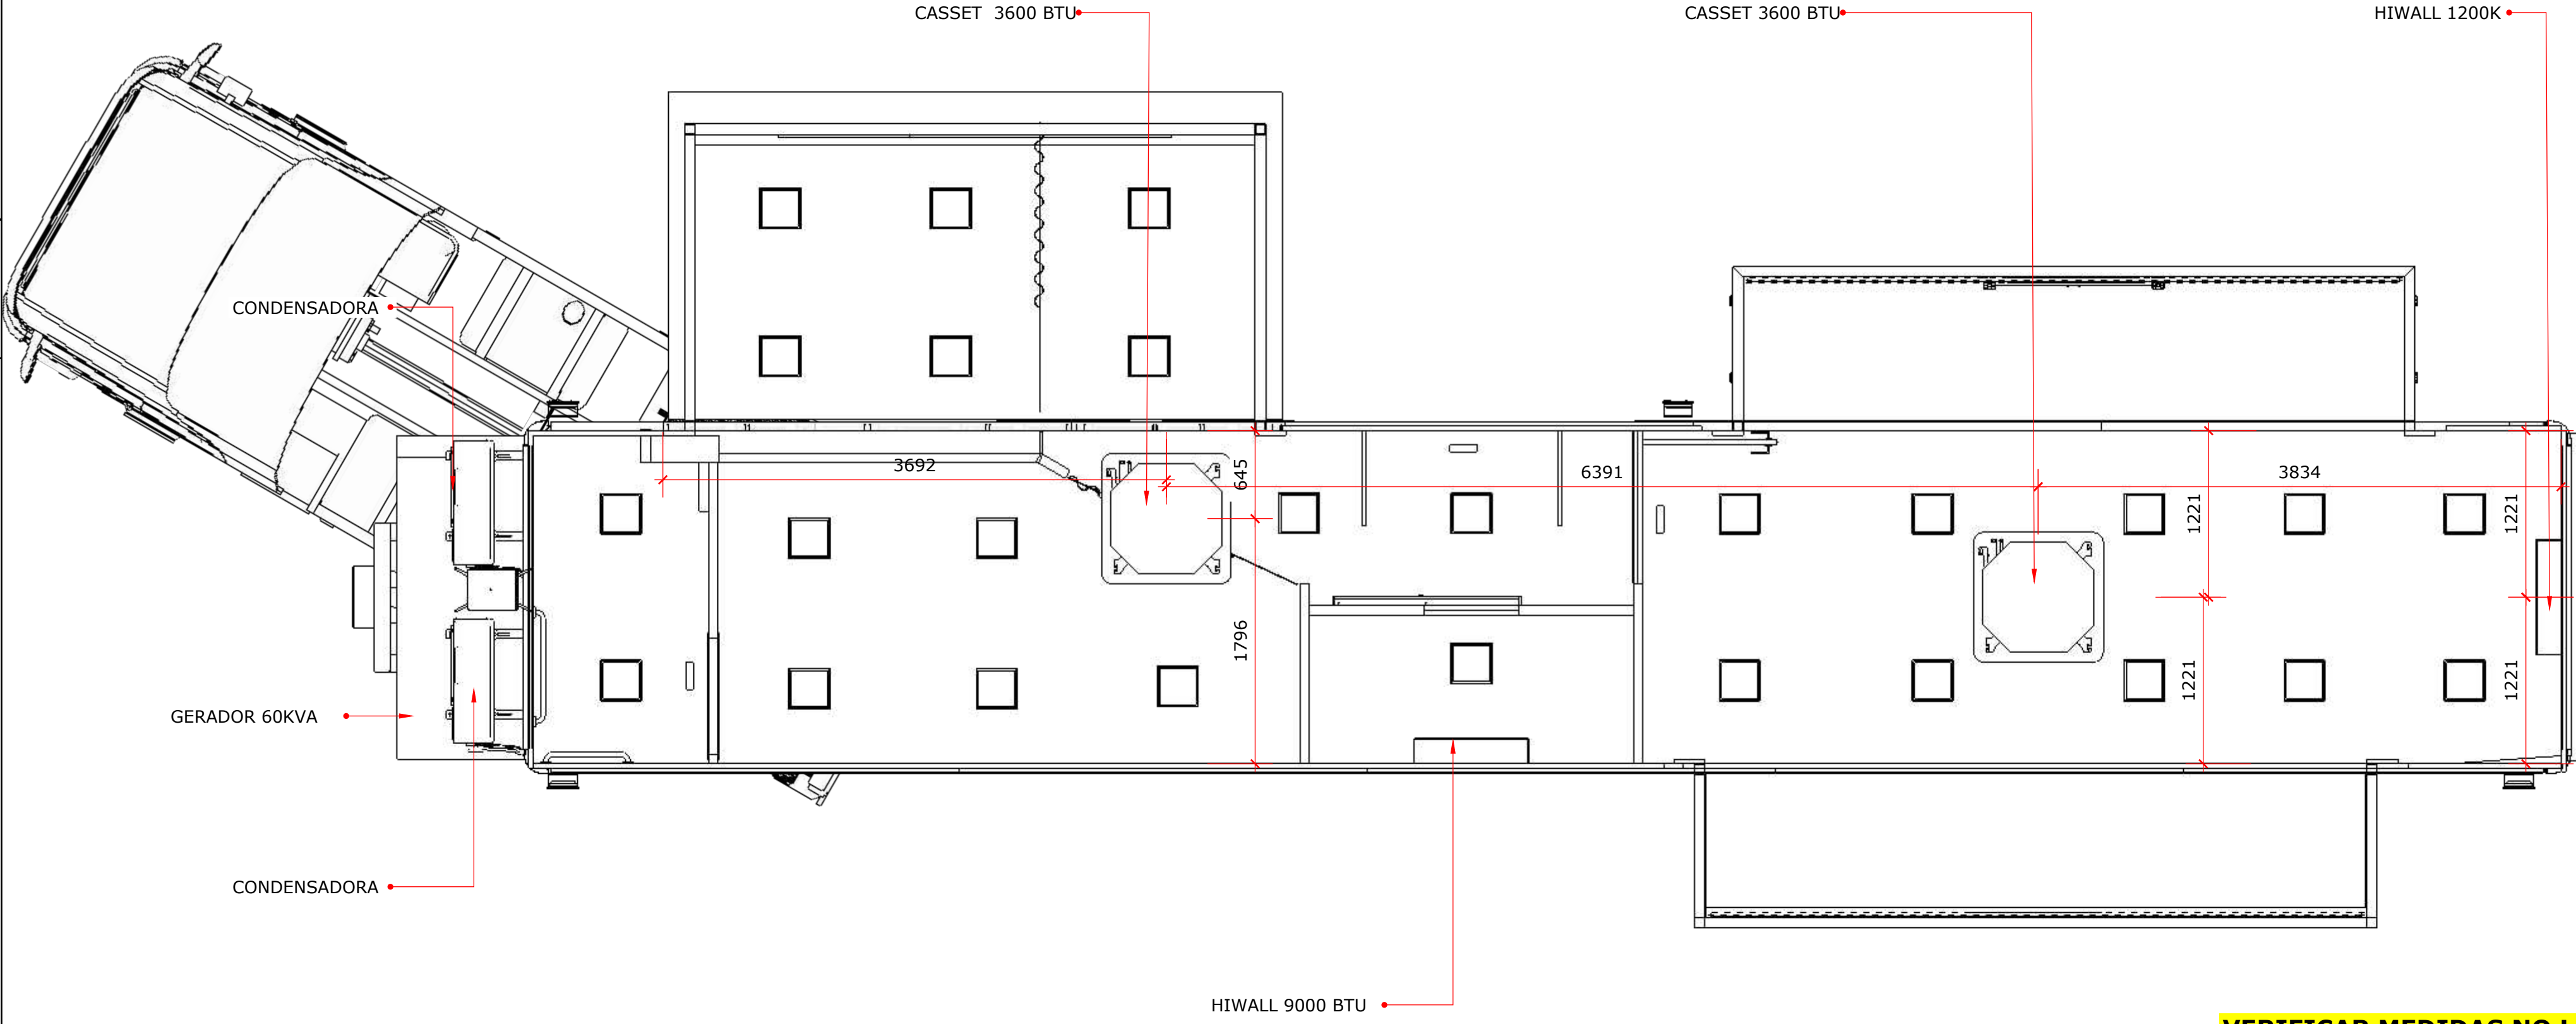

FASE	REVISÃO	DATA	DESCRIÇÃO DA REVISÃO	
PE	R00	20/07/2026	INICIAL	
OBS:				
Pedido:	15741	Ref. Comercial:	0.0.2026.1.7.4.AA	
Projeto:	360	Cliente:	BLUE HEALTH	
Arquivo:	PE-15741-R00	Aplicação:	CLIMATIZAÇÃO	
TRUCKVAN®		Escala:	1:40	
		Projetista:	Karla Souza	
		Aprovação:	Victor Dariano	
		Data:	20 / 07 / 2026	
				10
				17

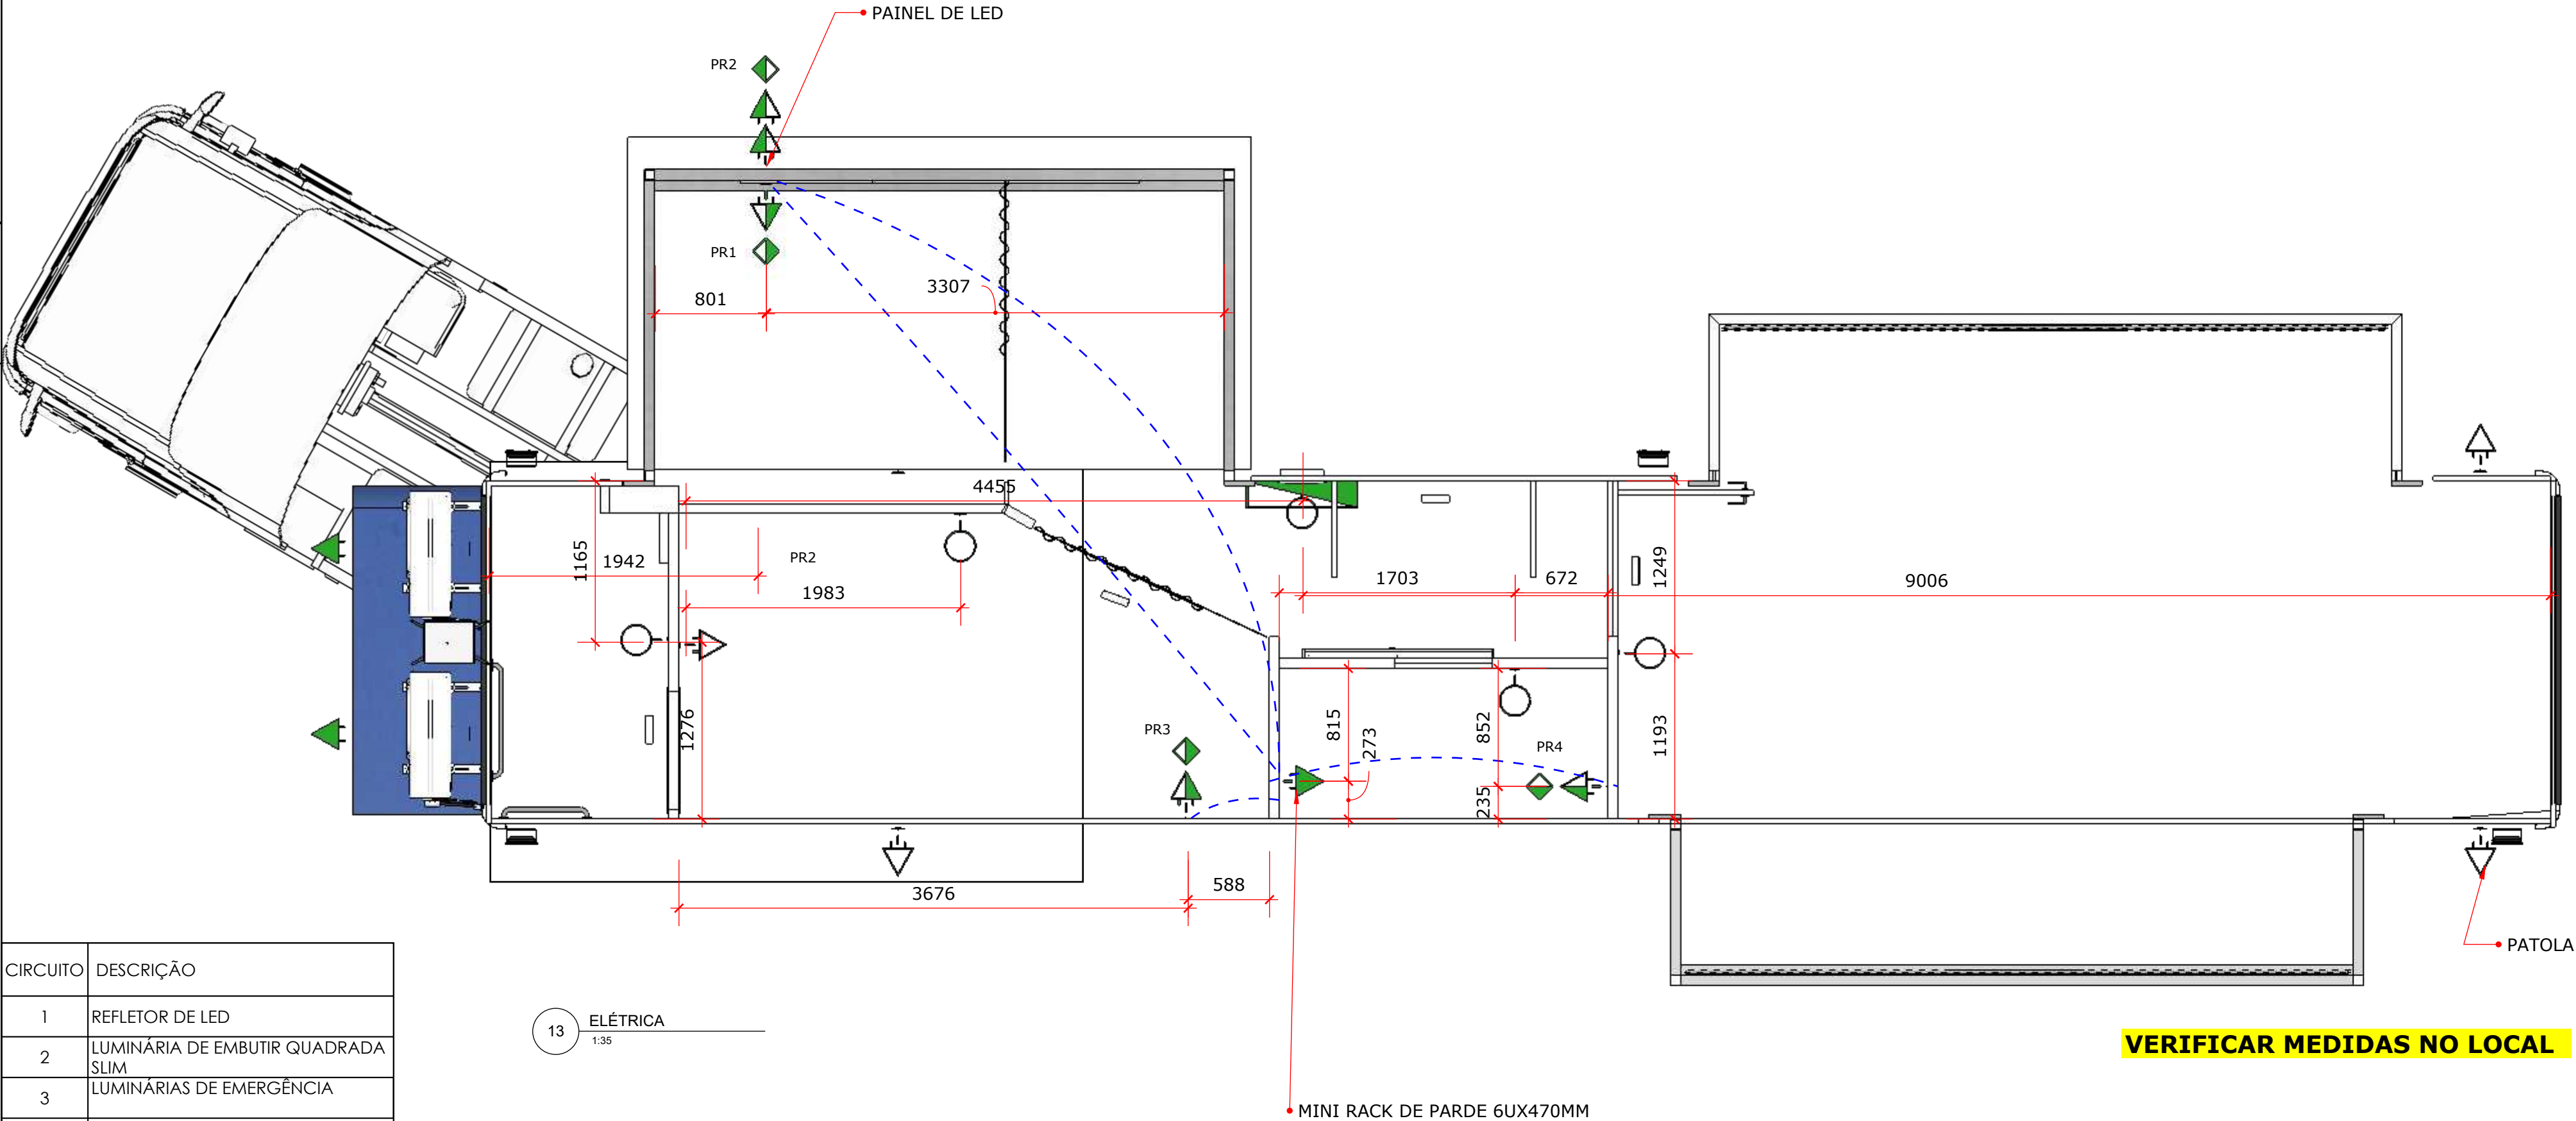



CIRCUITO	DESCRIÇÃO
1	REFLETOR DE LED
2	LUMINÁRIA DE EMBUTIR QUADRADA SLIM
3	LUMINÁRIAS DE EMERGÊNCIA
4	SWITCH 16 PORTAS
5	STARLINK
6	TOMÓGRAFO
7	
8	TUG
9	TUE (NOTEBOOKS)
10	LUMINÁRIA TARTARUGA
11	AR CONDICIONADO HI WALL 9000BTU
12	AR CONDICIONADO HI WALL 12000BTU
13	AR CONDICIONADO CASSETE 36000BTU
14	PLATAFORMA ELEVATORIA ONE ARM PADRAO 10501
15	CARREGADEORA DE BATERIA PARA PLATAFORMA
16	PORTA PCD
17	PAINEL DE LED - P3.9MM OUTDOOR
18	PROCESSADORA DE VIDEO TB10 WI-FI
19	SINALEIRO MAMOGRAFIA EM USO LUZ VERMELHA BIVOLT

13 ELÉTRICA
1:35


LEGENDA ELÉTRICA	
	Tomada 220V Alta - 200 cm do Piso
	Tomada 220V Média - 110 cm do Piso
	Tomada 220V Baixa - 30 cm do Piso
	Interruptor Simples - 110cm do Piso
	QDL - Quadro Geral

FASE	REVISÃO	DATA	DESCRIÇÃO DA REVISÃO	
PE	R00	20/07/2026	INICIAL	
OBS:				
Pedido:	15741	Ref. Comercial:	0.0.2026.1.7.4.AA	11
Projeto:	360	Cliente:	BLUE HEALTH	
Arquivo:	PE-15741-R00	Aplicação:	ELÉTRICA	17
		Escala:	1:40	
		Projetista:	Karla Souza	
		Aprovação:	Victor Dariano	
		Data:	20 / 07 / 2026	

14 VISTA SUPERIOR
1:10

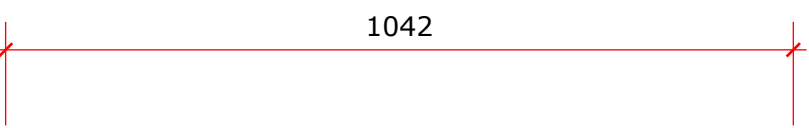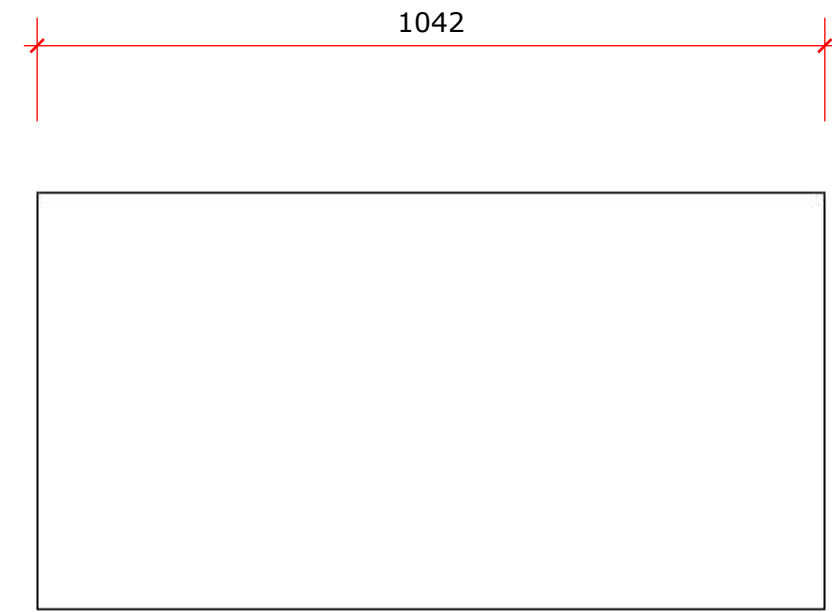


15 VISTA FRONTAL
1:10

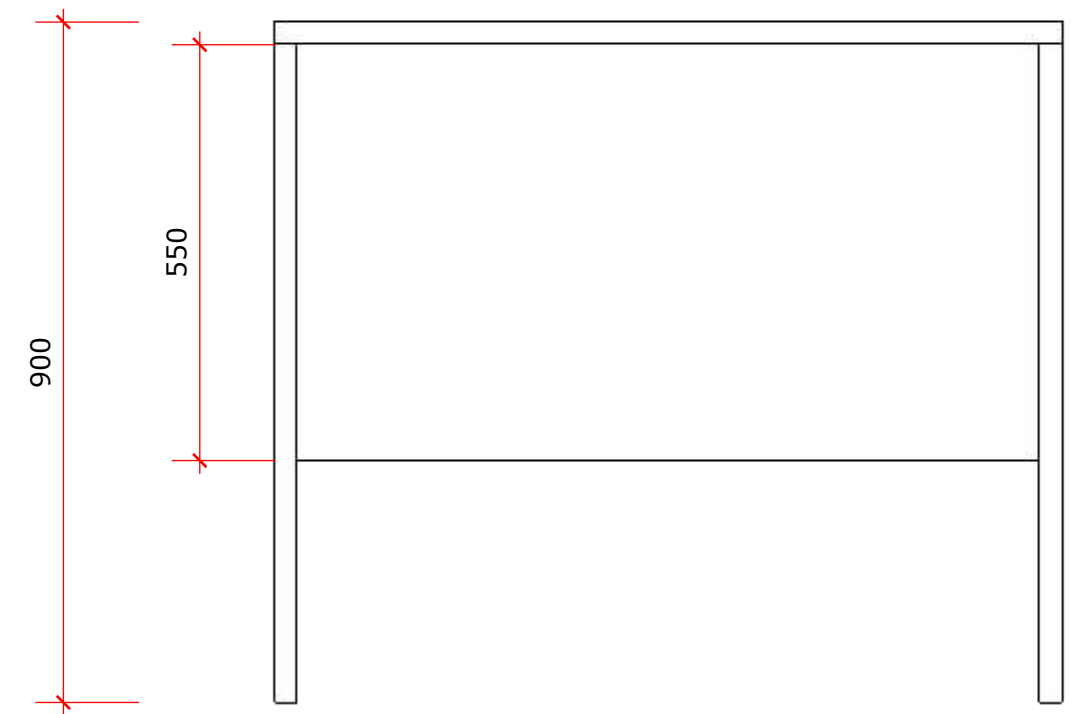


MDF BRANCO TX

16 PERSPECTIVA ISOMÉTRICA
1:60

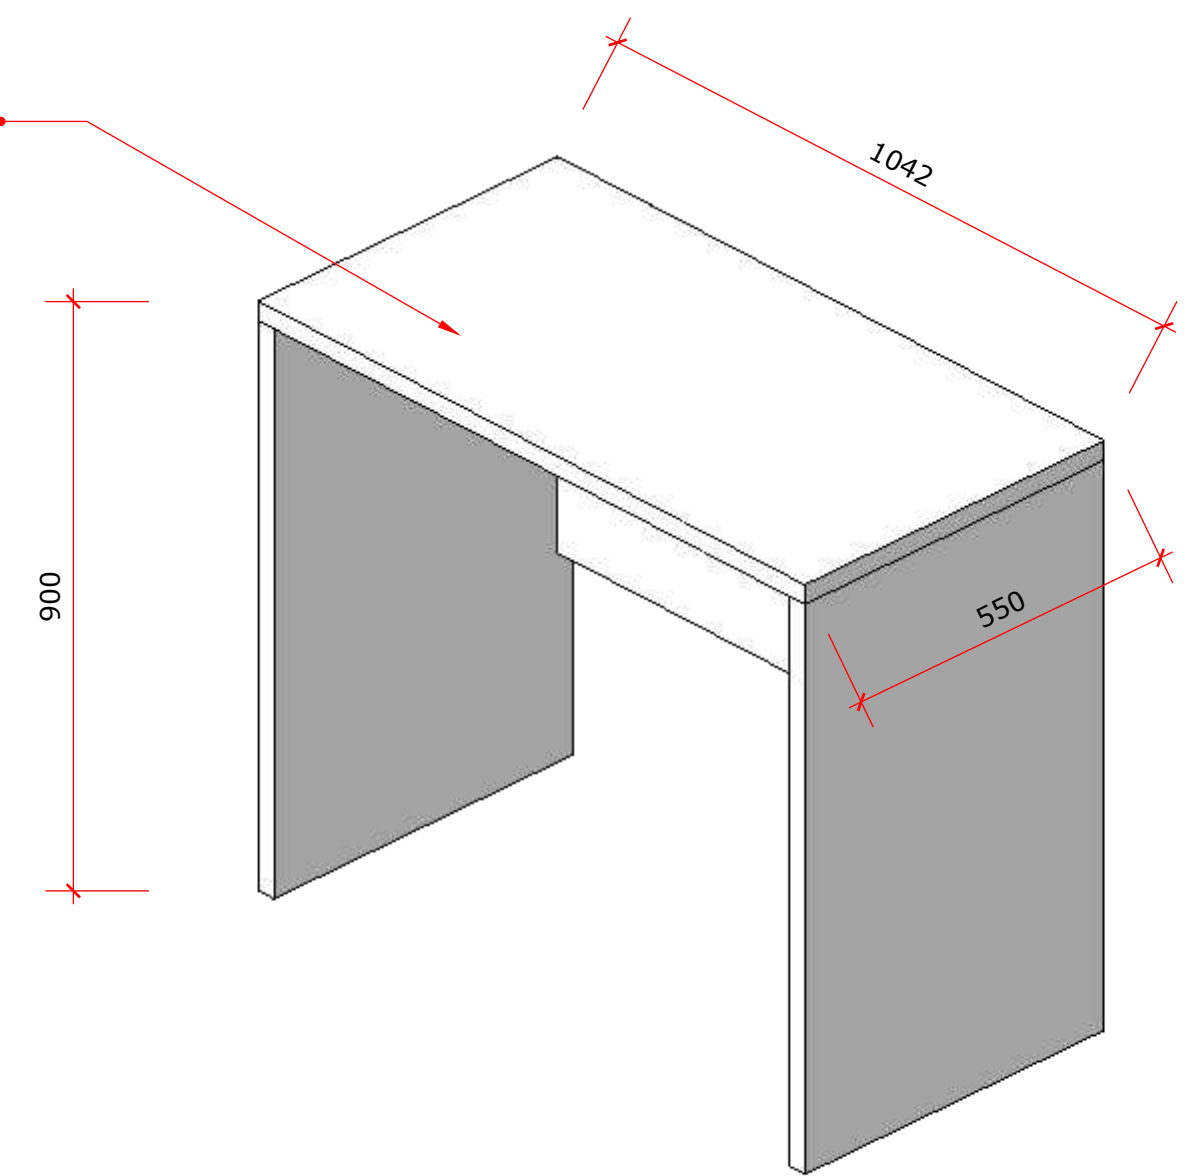


VERIFICAR MEDIDAS NO LOCAL

FASE	REVISÃO	DATA	DESCRIÇÃO DA REVISÃO	
PE	R00	20/07/2026	INICIAL	
OBS: INTERNO E EXTERNO SERÁ DE MDF BRANO TX 01 UNIDADE				
Pedido:	15741	Ref. Comercial:	0.0.2026.1.7.4.AA	12
Projeto:	360	Cliente:	BLUE HEALTH	
Arquivo:	PE-15741-R00	Aplicação:	MESA 1	17
			Escala:	1:40
			Projetista:	Karla Souza
			Aprovação:	Victor Dariano
			Data:	20 / 07 / 2026

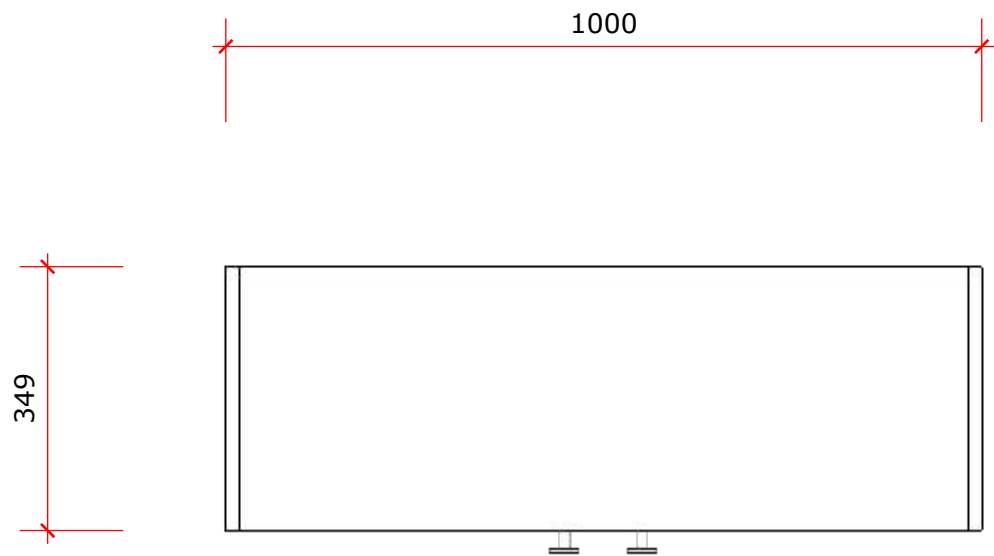


17 VISTA SUPERIOR
1:10

MDF BRANCO TX

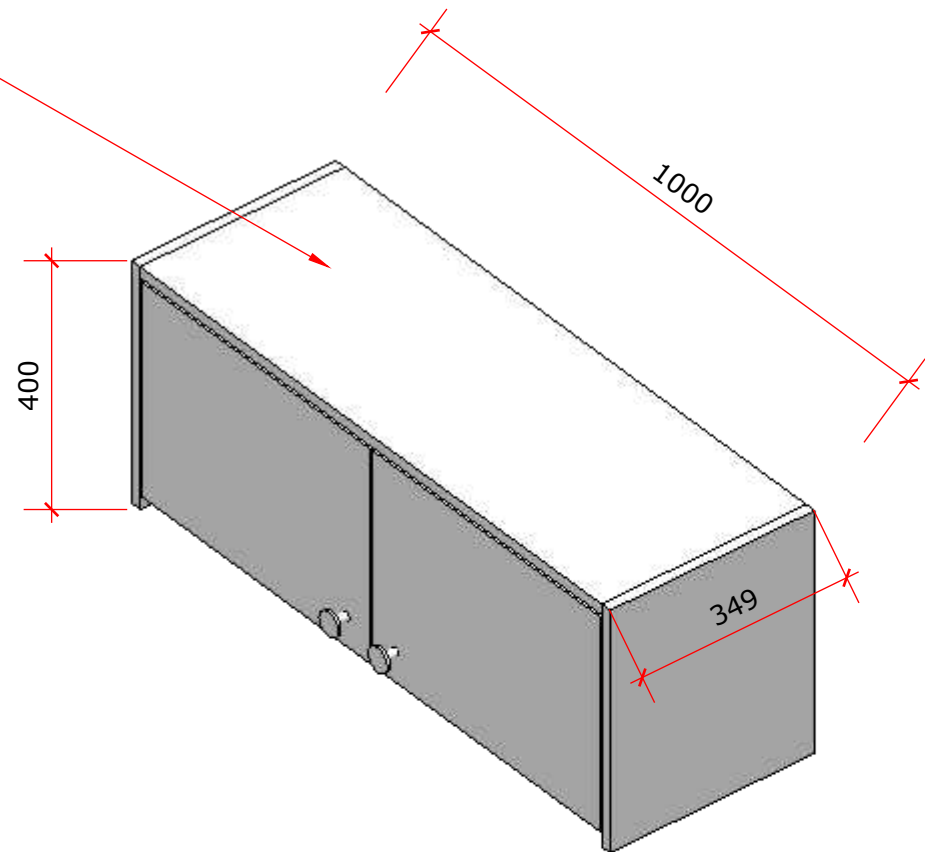


20 PERSPECTIVA ISOMÉTRICA
1:60

VERIFICAR MEDIDAS NO LOCAL

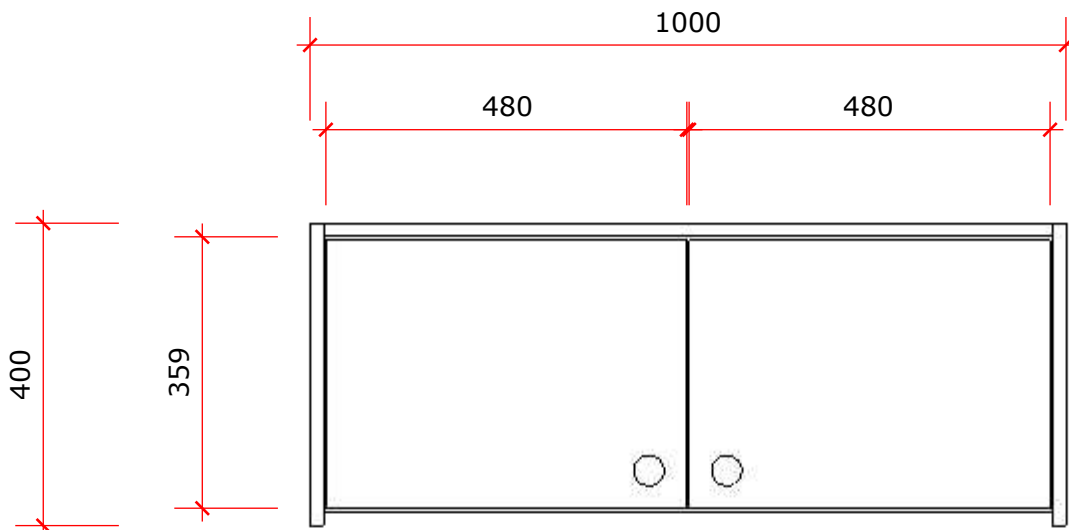


18 VISTA FRONTAL
1:10

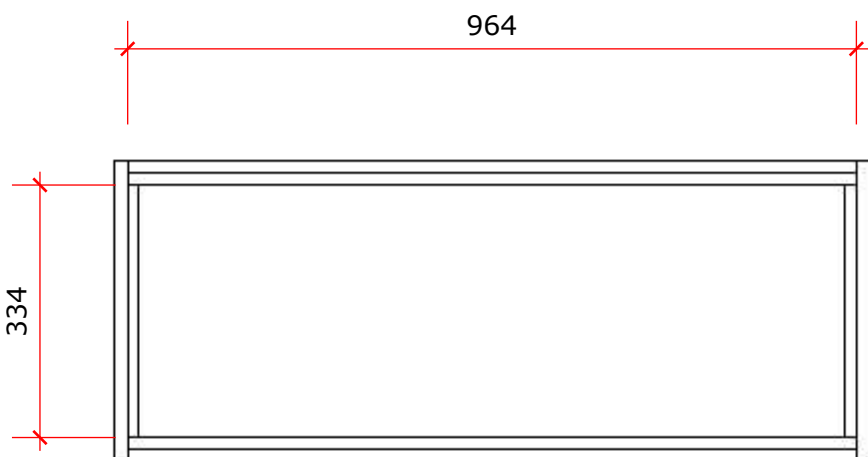


19 VISTA INTERNA
1:10


FASE	REVISÃO	DATA	DESCRIÇÃO DA REVISÃO	
PE	R00	20/07/2026	INICIAL	
OBS: INTERNO E EXTERNO SERÁ DE MDF BRANCO TX				
Pedido:	15741	Ref. Comercial:	0.0.2026.1.7.4.AA	13
Projeto:	360	Cliente:	BLUE HEALTH	
Arquivo:	PE-15741-R00	Aplicação:	ARMÁRIO 1	17
		Escala:	1:40	
		Projetista:	Karla Souza	
		Aprovação:	Victor Dariano	
		Data:	20 / 07 / 2026	

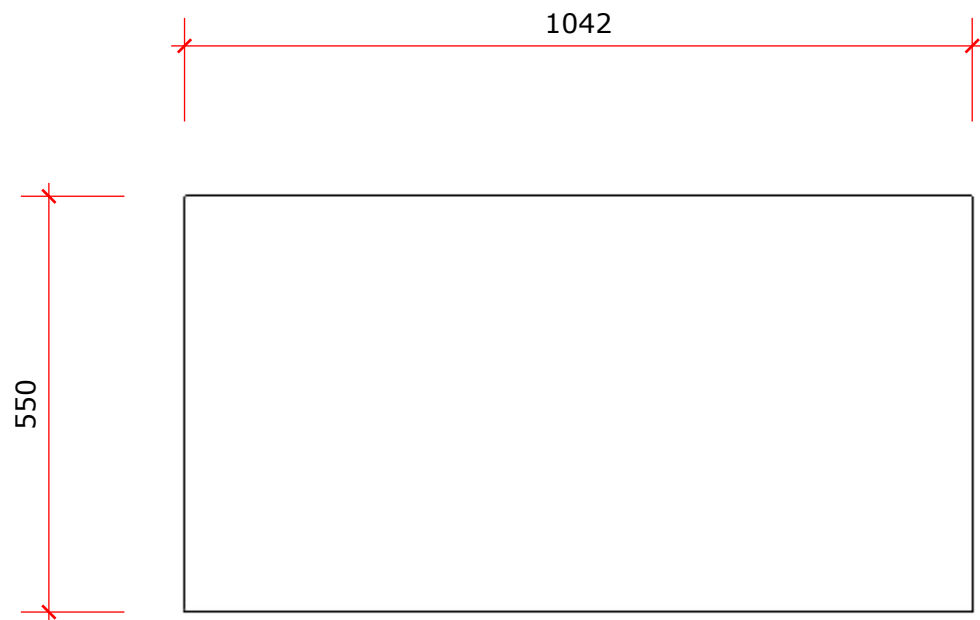

21 VISTA SUPERIOR
1:10

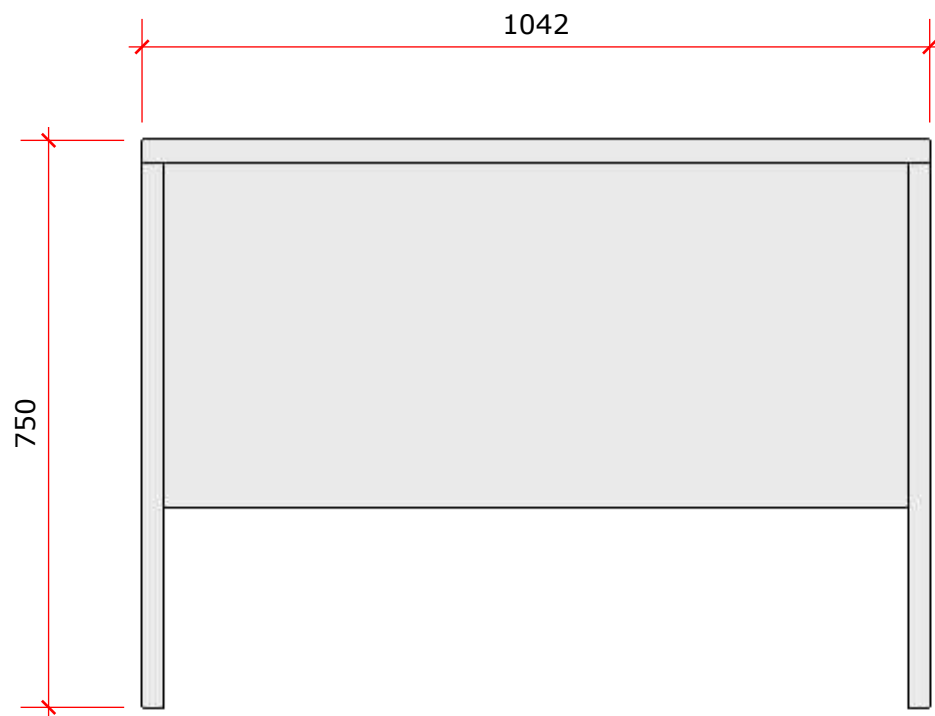


22 VISTA FRONTAL
1:10

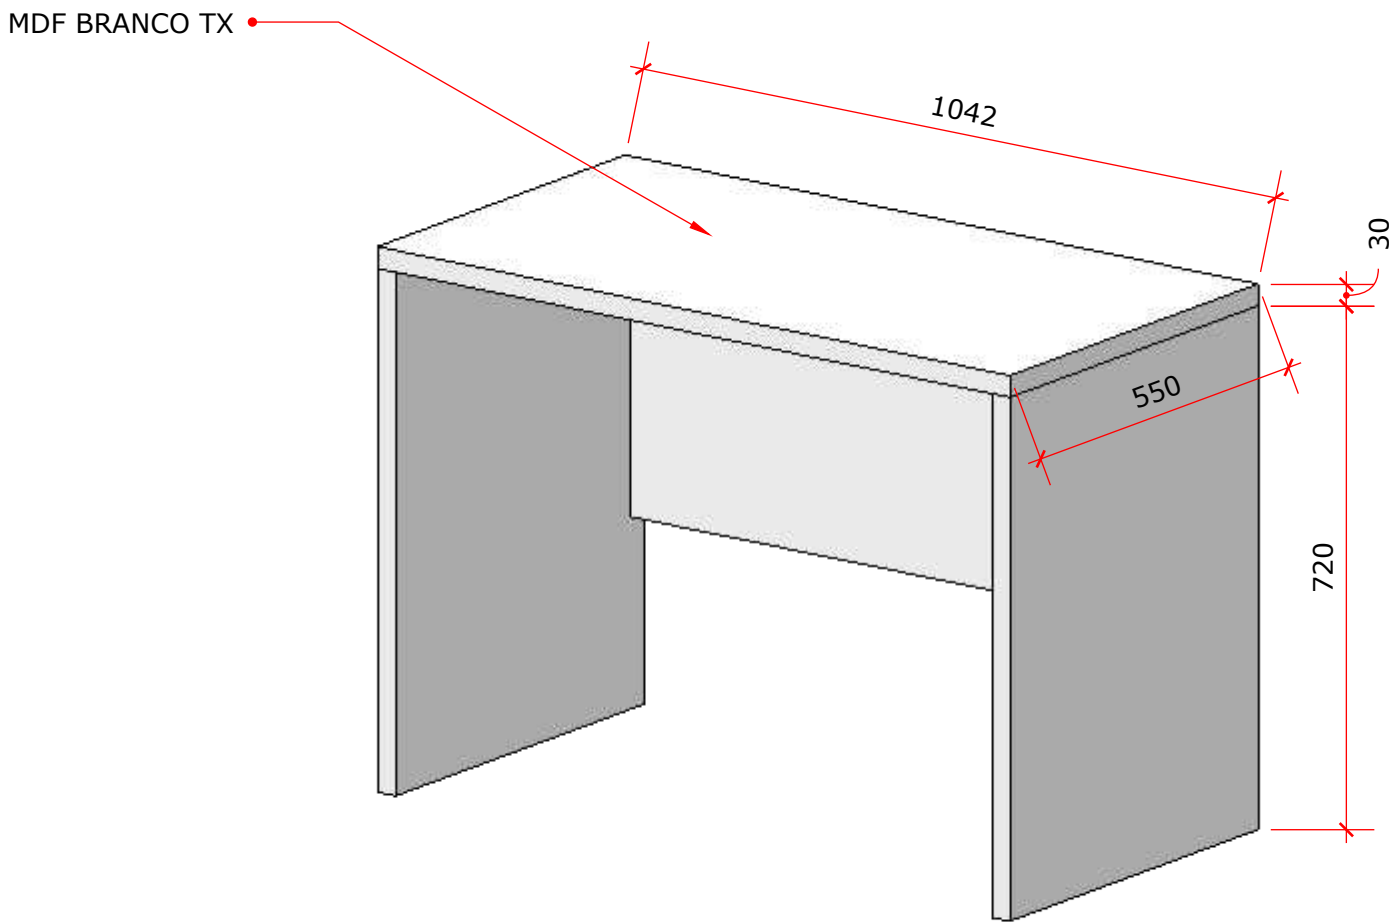


23 PERSPECTIVA ISOMÉTRICA
1:60

VERIFICAR MEDIDAS NO LOCAL


FASE	REVISÃO	DATA	DESCRIÇÃO DA REVISÃO	
PE	R00	20/07/2026	INICIAL	
OBS: INTERNO E EXTERNO SERÁ DE MDF BRANCO TX 01 UNIDADE				
Pedido:	15741	Ref. Comercial:	0.0.2026.1.7.4.AA	14
Projeto:	360	Cliente:	BLUE HEALTH	
Arquivo:	PE-15741-R00	Aplicação:	MESA 2	17
TRUCKVAN®	Escala:		1:40	
	Projetista:		Karla Souza	
	Aprovação:		Victor Dariano	
	Data:		20 / 07 / 2026	

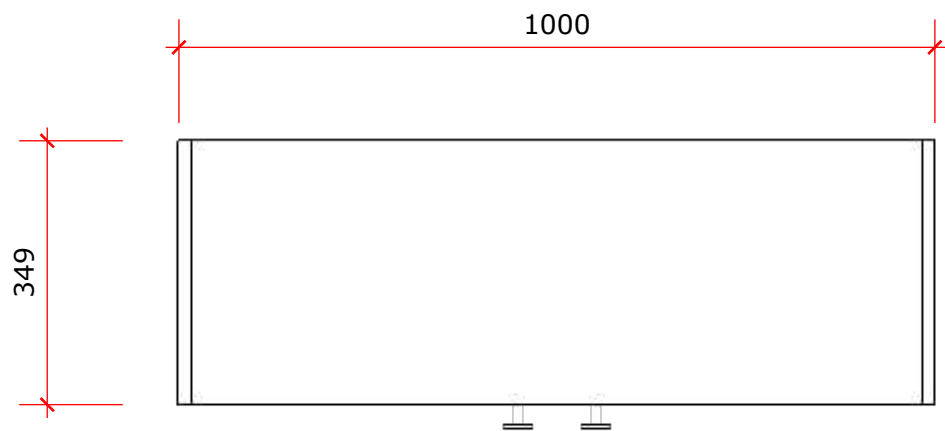

24 VISTA SUPERIOR
1:10

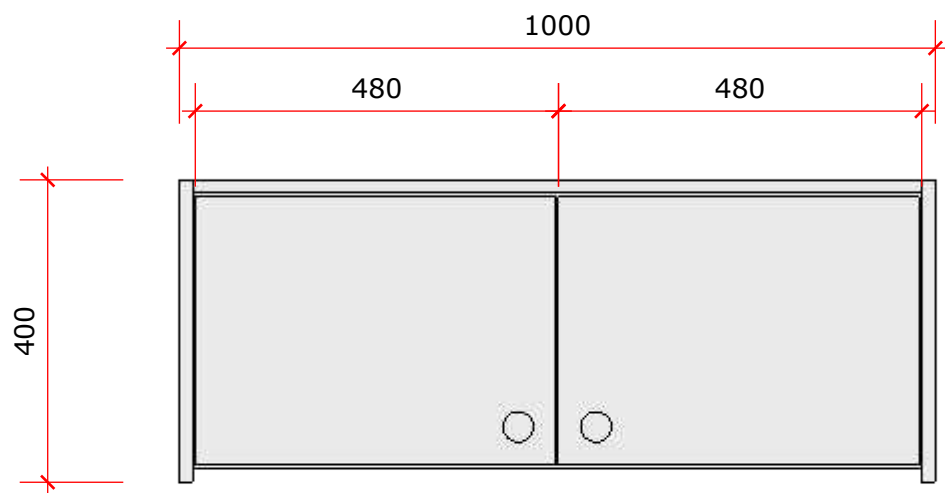


25 VISTA FRONTAL
1:10

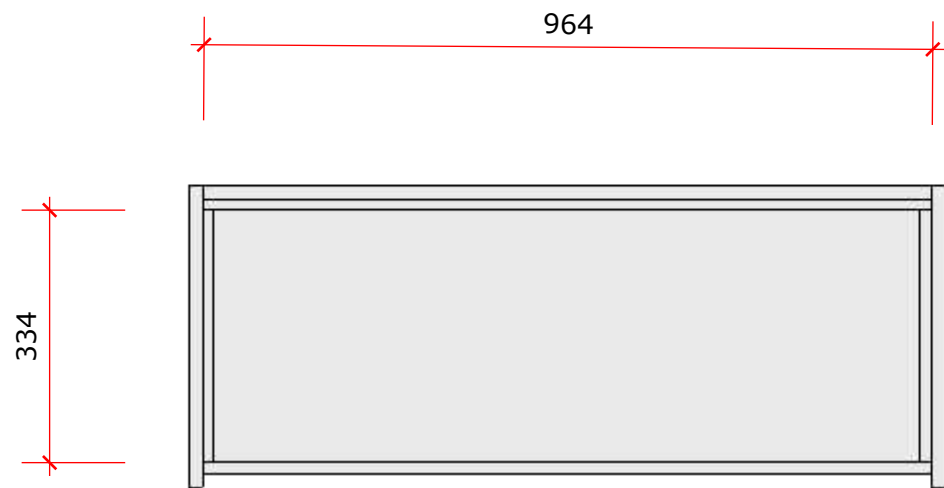

26 VISTA INTERNA
1:10


MDF BRANCO TX

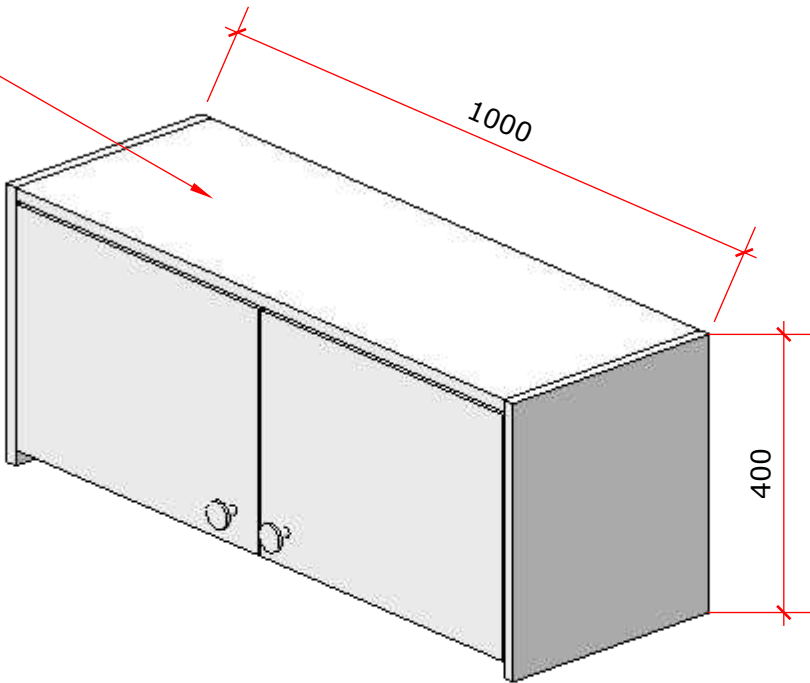


27 PERSPECTIVA ISOMÉTRICA
1:60

VERIFICAR MEDIDAS NO LOCAL


FASE	REVISÃO	DATA	DESCRIÇÃO DA REVISÃO	
PE	R00	20/07/2026	INICIAL	
OBS: INTERNO E EXTERNO SERÁ DE MDF BRANCO TX				
Pedido:	15741	Ref. Comercial:	0.0.2026.1.7.4.AA	15
Projeto:	360	Cliente:	BLUE HEALTH	
Arquivo:	PE-15741-R00	Aplicação:	ARMÁRIO 2	17
		Escala:	1:40	
		Projetista:	Karla Souza	
		Aprovação:	Victor Dariano	
		Data:	20 / 07 / 2026	

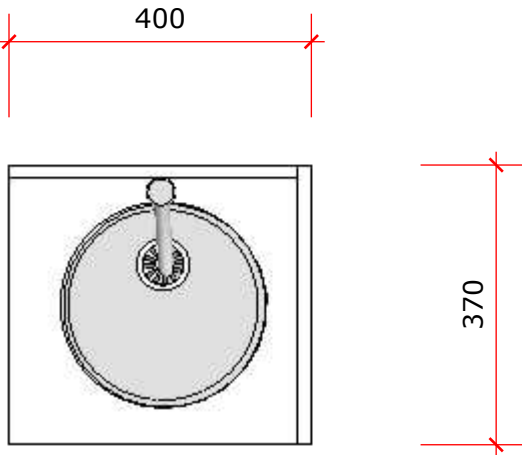

28 VISTA SUPERIOR
1:10

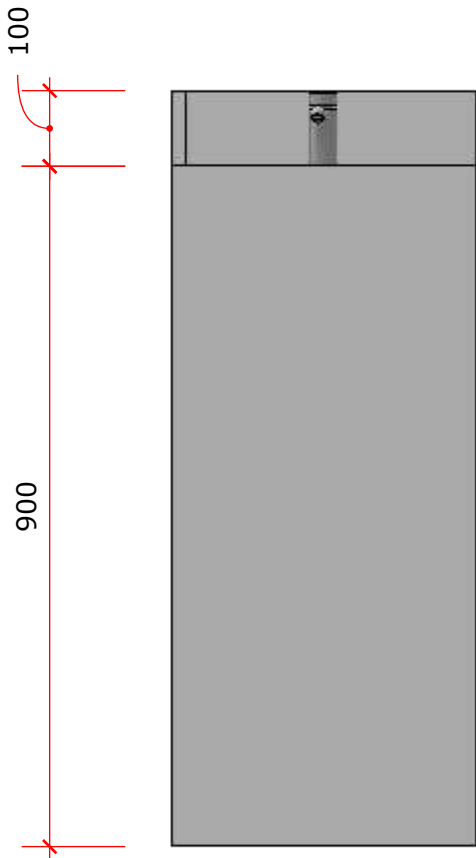


29 VISTA FRONTAL
1:10

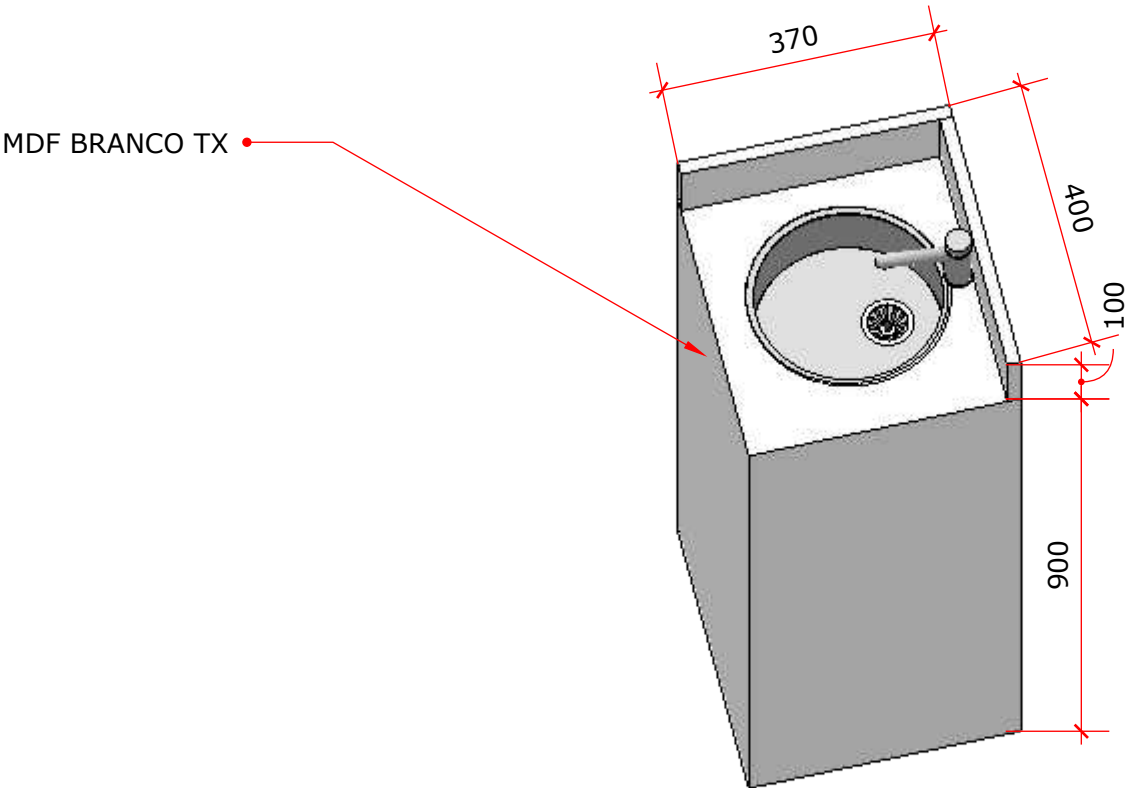


30 PERSPECTIVA ISOMÉTRICA
1:60

VERIFICAR MEDIDAS NO LOCAL

FASE	REVISÃO	DATA	DESCRIÇÃO DA REVISÃO	
PE	R00	20/07/2026	INICIAL	
OBS: INTERNO E EXTERNO SERÁ DE MDF BRANCO TX				
Pedido:	15741	Ref. Comercial:	0.0.2026.1.7.4.AA	16
Projeto:	360	Cliente:	BLUE HEALTH	
Arquivo:	PE-15741-R00	Aplicação:	GABINETE	17
		Escala:	1:40	
		Projetista:	Karla Souza	
		Aprovação:	Victor Dariano	
		Data:	20 / 07 / 2026	

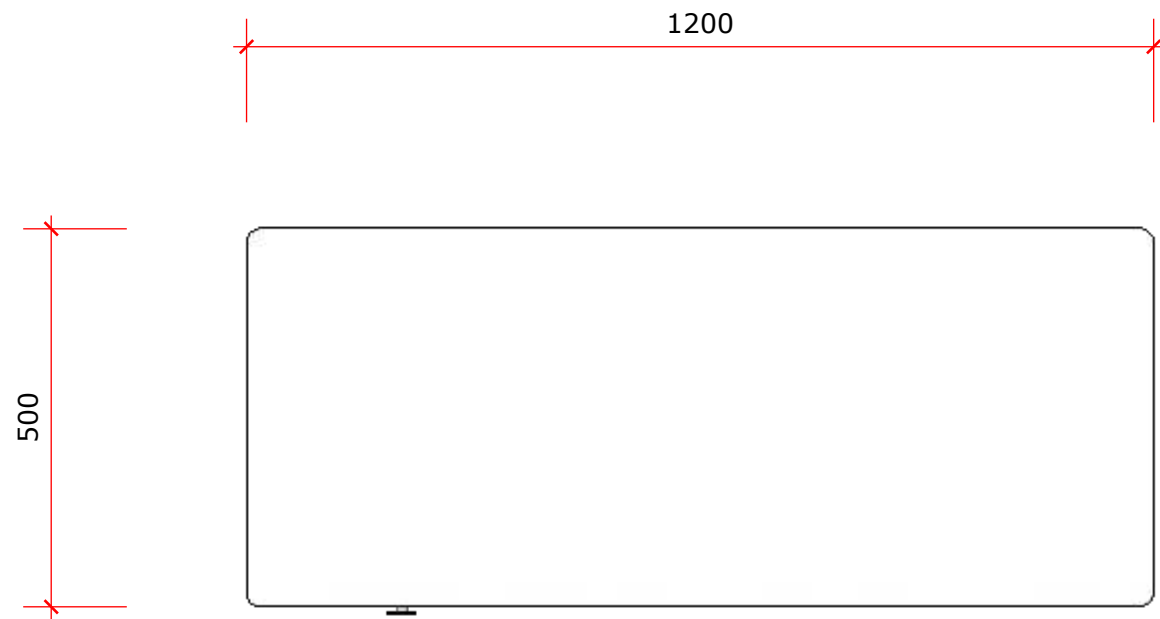


14 VISTA SUPERIOR
1:10

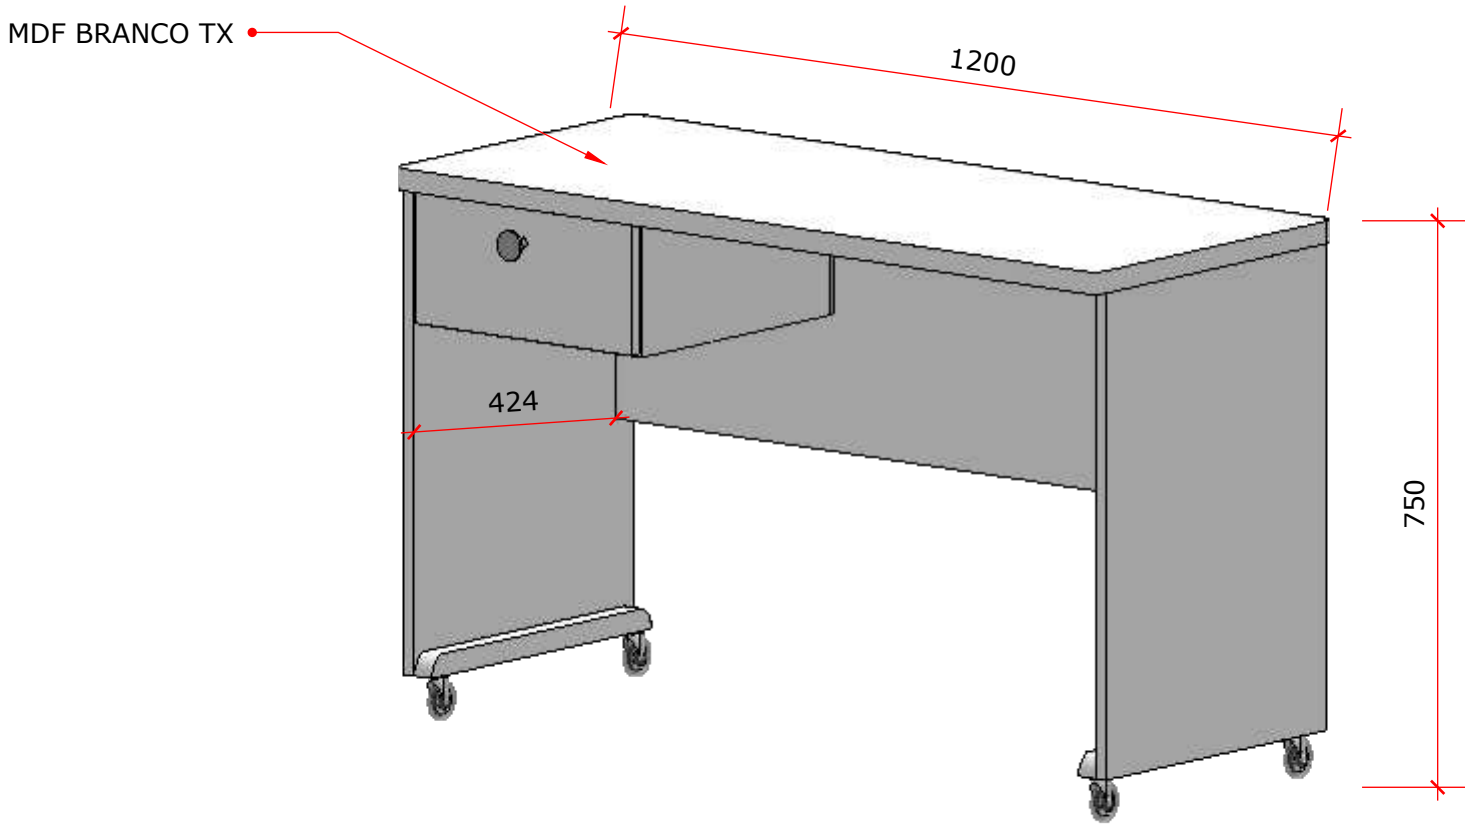

16 PERSPECTIVA ISOMÉTRICA
1:60

VERIFICAR MEDIDAS NO LOCAL

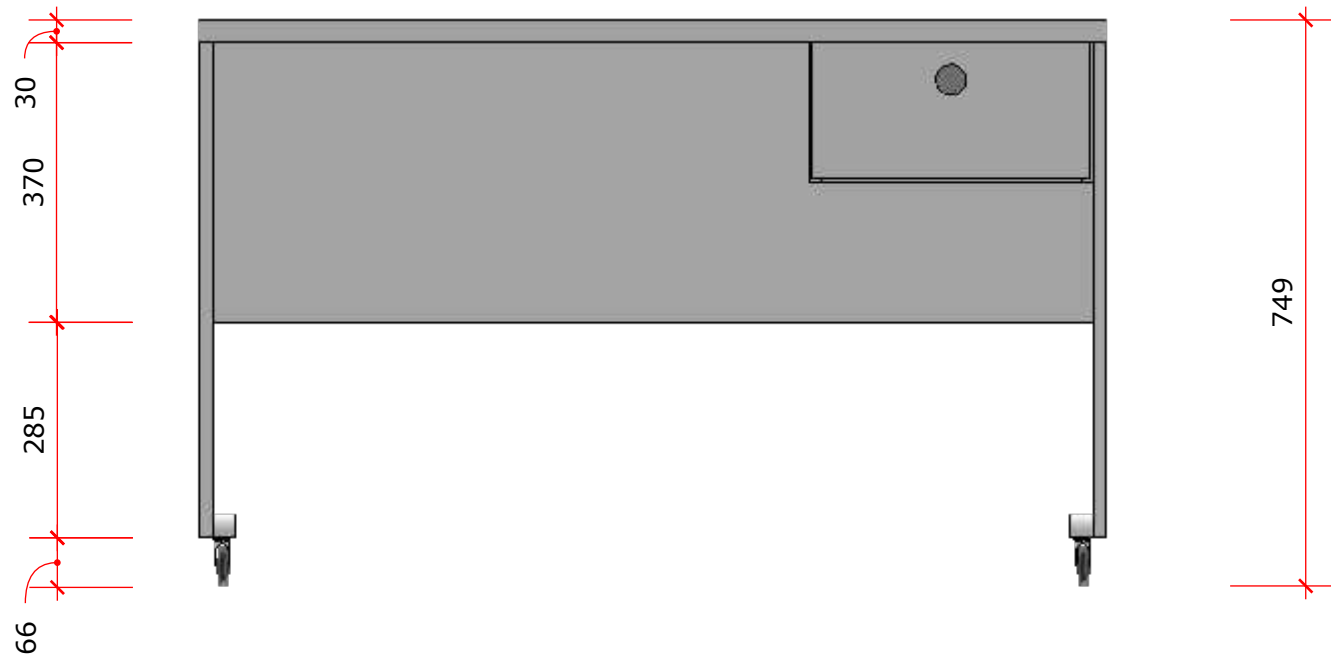

15 VISTA FRONTAL
1:10

FASE	REVISÃO	DATA	DESCRIÇÃO DA REVISÃO	
PE	R00	20/07/2026	INICIAL	
OBS: INTERNO E EXTERNO SERÁ DE MDF BRANO TX 02 UNIDADES				
Pedido:	15741	Ref. Comercial:	0.0.2026.1.7.4.AA	17
Projeto:	360	Cliente:	BLUE HEALTH	
Arquivo:	PE-15741-R00	Aplicação:	MESA SALA DE ATENDIMENTO	17
		Escala:	1:40	
		Projetista:	Karla Souza	
		Aprovação:	Victor Dariano	
		Data:	20 / 07 / 2026	